

**This plan/document forms part of the
Approved Construction Certificate
F2022-/00093
Issued By First Building Certifiers P/L BDC 3219**


1. ALL MATERIALS AND WORKMANSHIP TO BE IN ACCORDANCE WITH THE RELEVANT AND CURRENT S.A.A. CODES AND WITH THE BY-LAWS AND ORDINANCES OF THE RELEVANT BUILDING AUTHORITIES.
2. SETTING-OUT DIMENSIONS AND SIZES OF STRUCTURAL MEMBERS NOT TO BE OBTAINED BY SCALING THE STRUCTURAL DRAWINGS. ANY SETTING-OUT DIMENSIONS SHOWN IN THE STRUCTURAL DRAWINGS TO BE CHECKED BY THE CONTRACTOR BEFORE CONSTRUCTION COMMENCES. REFER ANY DISCREPANCY TO THE SUPERINTENDENT BEFORE PROCEEDING WITH THE WORK.
3. DURING CONSTRUCTION IT IS THE CONTRACTOR'S RESPONSIBILITY TO ENSURE THAT THE STRUCTURE IS MAINTAINED IN A SAFE AND STABLE CONDITION AND NO PART IS OVERSTRESSED. TEMPORARY BRACING TO BE PROVIDED BY THE CONTRACTOR AS REQUIRED TO KEEP THE WORKS AND EXCAVATIONS STABLE AT ALL TIMES.
4. UNLESS NOTED OTHERWISE, ALL LEVELS ARE IN METRES AND ALL DIMENSIONS ARE IN MILLIMETRES.
5. THE STRUCTURAL COMPONENTS DETAILED ON THESE DRAWINGS HAVE BEEN DESIGNED IN ACCORDANCE WITH THE RELEVANT S.A.A. CODES AND BUILDING CODE OF AUSTRALIA FOR THE FOLLOWING LOADINGS:-

ELEMENT	LIVE LOAD (kPa)
NON TRAFFICABLE ROOF	0.25 (U.N.O.)
SUSPENDED SLABS	2.0 (U.N.O.)
SUPERIMPOSED	1.0 (U.N.O.)


EARTHQUAKE LOADING HAS BEEN DETERMINED IN ACCORDANCE WITH AS 1170.4

6. ALL MATERIALS AND WORKMANSHIP SHALL BE IN ACCORDANCE WITH THE CURRENT CODES OF PRACTICE EXCEPT WHERE VARIED BY THE SPECIFICATION AND/OR DRAWINGS.
- AS 3600 CONCRETE STRUCTURES CODE
 - AS 4671 STEEL REINFORCING MATERIALS
 - AS 4100 STEEL STRUCTURES CODE
 - AS 1302 STEEL REINFORCING BARS FOR CONCRETE
 - AS 1163 STRUCTURAL STEEL HOLLOW SECTIONS
 - AS 1554 (PART 1.) WELDING IN BUILDINGS
 - AS 1720.1 TIMBER ENGINEERING CODE
 - AS 1289 METHODS OF TESTING SOILS FOR ENGINEERING PURPOSES
 - AS 3700 MASONRY CODE
 - AS 3798 GUIDELINES FOR EARTHWORKS FOR COMMERCIAL AND RESIDENTIAL DEVELOPMENTS
 - AS 3610 FORMWORK FOR CONCRETE

1. FOOTINGS HAVE BEEN DESIGNED FOR AN ALLOWABLE BEARING INTENSITY OF 100kPa. ON STABLE NATURAL MATERIAL. TO BE CONFIRMED ON SITE FOUNDATION MATERIAL TO BE APPROVED FOR THIS PRESSURE BY THE ENGINEER & BUILDING AUTHORITY BEFORE REINFORCEMENT AND/OR CONCRETE ARE PLACED.
2. FOOTINGS TO BE LOCATED CENTRALLY UNDER WALLS AND COLUMNS U.N.O.
3. RETAINING WALLS (OTHER THAN CANTILEVER WALLS) NOT TO BE BACKFILLED UNTIL FLOOR CONSTRUCTION AT TOP AND BOTTOM IS COMPLETED. ENSURE FREE DRAINING BACKFILL IS USED, AND DRAINAGE IS IN PLACE. CANTILEVER WALLS TO BE BACKFILLED ONLY AFTER MINIMUM CONCRETE STRENGTH IS ACHIEVED.
4. BLINDING CONCRETE TO BE PLACED ON THE SAME DAY AS THE FINAL EXCAVATION TO THE FOUNDATION DESIGN LEVEL.
5. FOOTING LEVELS, WHERE SHOWN, ARE ESTIMATES ONLY AND WILL BE ESTABLISHED DURING SITE INSPECTION.
6. UNLESS OTHERWISE APPROVED BY THE ENGINEER THE LIMITATIONS OF EXCAVATIONS NEAR FOOTINGS SHALL BE AS FOLLOWS:-

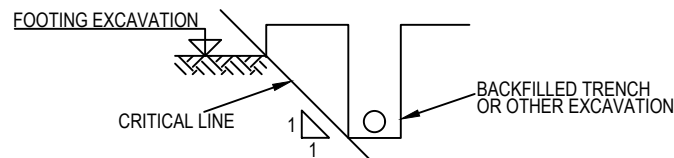

SUB GRADE AND SUB BASE FOR SLABS ON GROUND SHALL COMPLY WITH THE FOLLOWING:-

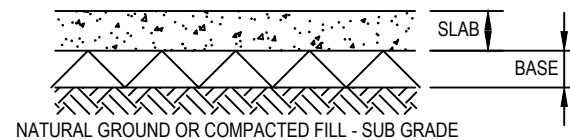

1. NO PENETRATIONS OR CHASES SHALL BE MADE IN MASONRY WALLS OR OTHER STRUCTURE WITHOUT APPROVAL OF THE STRUCTURAL ENGINEER.

1. ALL WORKMANSHIP AND MATERIALS TO BE IN ACCORDANCE WITH A.S.3600 AND THE CONCRETE SPECIFICATION.
2. CONCRETE QUALITY:-

ELEMENT	SLUMP	MAX. SIZE AGGREGATE	CEMENT TYPE	CONCRETE GRADE
FOUNDATIONS	80	20	GP	25MPa
SLAB ON GROUND	80	20	GP	25MPa
SUSPENDED SLAB	80	20	GP	25MPa

PROJECT CONTROL TESTING TO BE CARRIED OUT IN ACCORDANCE WITH A.S.3600.

3. NO ADMIXTURES TO BE USED IN CONCRETE UNLESS APPROVED IN WRITING.
4. CONCRETE DIMENSIONS SHOWN DO NOT INCLUDE THICKNESSES OF APPLIED FINISHES.
5. DEPTHS OF BEAMS ARE GIVEN FIRST AND INCLUDE SLAB THICKNESS.
6. ALL EXPOSED EDGES AND CORNERS TO BE PROVIDED WITH 25mm FILLETS OR CHAMFERS. MAINTAIN COVER TO REINFORCEMENT AT THESE DETAILS UNLESS OTHERWISE INDICATED.
7. NO HOLES, CHASES OR EMBEDMENT OF PIPES OTHER THAN THOSE SHOWN ON THE STRUCTURAL DRAWINGS TO BE MADE IN CONCRETE MEMBERS WITHOUT THE PRIOR WRITTEN APPROVAL OF THE ENGINEER.
8. CONSTRUCTION JOINTS WHERE NOT SHOWN TO BE LOCATED TO THE APPROVAL OF THE ENGINEER. DETAILS OF CONSTRUCTION JOINTS TO BE SUBMITTED TO THE ENGINEER FOR APPROVAL.
9. THE FINISHED CONCRETE TO BE A DENSE HOMOGENEOUS MASS, COMPLETELY FILLING THE FORMWORK THOROUGHLY EMBEDDING THE REINFORCEMENT AND FREE OF STONE POCKETS. ALL CONCRETE INCLUDING SLABS ON GROUND AND FOOTINGS, TO BE COMPACTED WITH MECHANICAL VIBRATORS.
10. CURING OF ALL CONCRETE TO BE ACHIEVED BY KEEPING SURFACES CONTINUOUSLY WET FOR A PERIOD OF 3 DAYS, AND PREVENTION OF LOSS OF MOISTURE FOR A TOTAL OF 7 DAYS FOLLOWED BY A GRADUAL DRYING OUT. APPROVED SPRAYED OR CURING COMPOUNDS MAY BE USED WHERE NO FLOOR FINISH IS PROPOSED. POLYTHENE SHEETING OR WET HESSIAN MAY BE USED IF PROTECTED FROM WIND AND TRAFFIC.
11. CONSTRUCTION SUPPORT PROPPING TO BE LEFT IN PLACE WHERE NEEDED TO AVOID OVERSTRESSING THE STRUCTURE DUE TO CONSTRUCTION LOADING.
12. CONDUITS, PIPES ETC, ONLY TO BE LOCATED AS SHOWN IN THE DRAWINGS OR AS APPROVED BY THE ENGINEER.
13. ALL FORMWORK AND PROPPING UNDER SUSPENDED CONCRETE WORKS SHALL BE REMOVED BEFORE ANY MASONRY WORK IS BUILT ABOVE.
14. CAMBERS, UNLESS NOTED OTHERWISE ON THE DRAWINGS AND EXCEPT FOR PRESTRESSED WORK SHALL BE PROVIDED IN BEAMS AND SLABS AS FOLLOWS:-
 - i) SPANS - $0.002 \times \text{SPAN}$
 - ii) CANTILEVERS - $0.004 \times \text{CANTILEVER LENGTH}$CAMBERS SHALL BE CHECKED BEFORE AND AFTER DEPROPPING TO DETERMINE THE DEFLECTION OF THE MEMBERS UNDER THEIR SELF WEIGHT. PROVISION SHALL BE MADE IN THE FORMWORK SYSTEM FOR THE STRUCTURAL ENGINEER TO VARY THE SPECIFIED CAMBERS ON THE BASIS OF THIS INFORMATION. THE TOP SURFACE OF A CAMBERED MEMBER SHALL BE FINISHED TO MAINTAIN THE SPECIFIED DEPTH OF THE MEMBER.
15. SHRINKAGE
MAXIMUM DRYING SHRINKAGE STRAIN MEASURED IN ACCORDANCE WITH AS 1012 PART 13 SHALL NOT EXCEED 650×10^{-6} AT 8 WEEKS
16. BACKPROPPING FOR FORMWORK TO BE DESIGNED IN ACCORDANCE WITH AS 1509 AND SUBMITTED FOR ENGINEER'S COMMENTS
17. THE STRUCTURAL DESIGN FOR SUSPENDED STRUCTURES ASSUMES:-
 1. A MAXIMUM COMBINED VERTICAL DEFLECTION OF FORMWORK AND PROPS OF 2mm UNDER THE WEIGHT OF CONCRETE, REINFORCEMENT AND CONSTRUCTION LIVE LOAD.
 2. REMOVAL OF FORMWORK AND PROPS SHALL COMPLY WITH CLAUSE 19.6.2 OF AS3600

[illegible]

TIMBER NOTES:

1. ALL TIMBER DESIGN, CONSTRUCTION & MATERIAL TO BE TO AS 1720 & NEW SOUTH WALES TIMBER FRAMING MANUAL.
2. AS 1684 SHALL BE APPLIED TO DOMESTIC CONSTRUCTION IN SHELTERED LOCATIONS.
3. SOFTWOOD TO BE MINIMUM GRADE F7 U.N.O. HARDWOOD TO BE MINIMUM GRADE F14.
4. EXTERNAL TIMBER TO BE EITHER HARDWOOD DURABILITY CLASS 1 OR CLASS 2 AS PER AS 1720.2 OR IMPREGNATED PINE GRADE F7, PRESSURE TREATED TO AS 1604 & RE-DRIED PRIOR TO USE. SUPPLEMENTARY TREATMENT SHALL BE APPLIED TO ALL CUT SURFACES. SUPPLY SUPPORTING DOCUMENTATION FOR PRESERVATIVE TREATMENT.
5. ALL BOLTS IN TIMBER CONSTRUCTION TO BE MINIMUM M16 U.N.O. BOLT HOLES TO BE DRILLED EXACT SIZE. WASHERS UNDER HEADS AND NUTS TO BE AT LEAST 2.5 TIMES BOLT DIAMETER.
6. TIMBER DIMENSIONS ON THE FINISHED WIDTH & THICKNESS TO BE:
 - SEASONED SOFTWOOD +5,-0mm
 - UNSEAONED SOFTWOOD >F7+3,-3mm.LESS THAN OR EQUAL TO F7+2,-4mm
 - SEASONED SOFTWOOD +2,-0mm
 - UNSEAONED SOFTWOOD +3,-3mm (SEE ALSON CLAUSE 1.6.2 IN AS 2082).
8. ALL TIMBER JOINT & NOTCHES ARE TO BE 100mm MINIMUM AWAY FROM LOOSE KNOTS, SEVERE SLOPING GRAIN, GUM VEINS OR OTHER MINOR DEFECTS.


<u>TIMBER DURABILITY</u>		
LOCATION	HAZARD CLASS (SOFT WOODS)	DURABILITY CLASS (HARD WOODS)
INTERNAL ABOVE GROUND	H2	CLASS 1 OR 2
EXTERNAL ABOVE GROUND	H3	CLASS 1 OR 2
BELOW GROUND	H5	CLASS 1

STRUCTURAL STEEL

1. ALL WORKMANSHIP AND MATERIALS TO BE IN ACCORDANCE WITH A.S.4100 AND A.S.1554.
2. UNLESS OTHERWISE NOTED, ALL STEEL TO BE GRADE 300 (HOLLOW SECTIONS TO BE GRADE 350).
3. ALL CONNECTION AND STIFFENER PLATES TO BE 10mm THICK U.N.O.
4. ALL WELDS TO BE 6mm CONTINUOUS FILLET SPECIAL PURPOSE WELDS U.N.O.
ALL WELDING TO BE SP U.N.O. FROM E41XX(ELECTRODES)/W48X(WIRE)
5. ALL BOLTS TO BE M20 AND NO CONNECTION TO HAVE LESS THAN 2 BOLTS U.N.O.
6. ALL BOLTS TO BE GALVANISED GRADE 8.8/S U.N.O.
7. PURLIN CONNECTIONS TO BE AS PER MANUFACTURER'S SPECIFICATION U.N.O.
8. ALL HOLDING DOWN BOLTS TO BE GALVANISED GRADE 4.6/S U.N.O.
9. STRUCTURAL STEEL ITEMS WHICH ARE PROTECTED FROM WEATHER TO BE ABRASIVE BLAST CLEANED TO CLASS 2.5 TO AS 1627.4, TO BE PRIMED BY INTERZINC 7 OR APPROVED EQUIVALENT TO 75mm DFT. ALL OTHER STRUCTURAL STEEL ITEM TO BE FULLY GALVANISED TO A.S.1650 U.N.O. ON THE DRAWINGS. REFER TO ARCHITECTURAL DETAILS FOR TOP COATS.
10. SHOP DRAWINGS TO BE SUBMITTED IN TRIPLICATE TO THE ENGINEER/DESIGNER FOR APPROVAL. FABRICATION NOT TO COMMENCE UNTIL APPROVAL HAS BEEN GIVEN.
10. EXAMINATION OF WELDS TO BE (INSPECTION AND TEST RECORDS TO BE SUBMITTED TO THE ENGINEER):-
 - VISUAL SCANNING TO AS1554.1 APPENDIX F ON 100% OF WELDS;
 - VISUAL EXAMINATION TO A.S.1554.1 APPENDIX F ON 10% OF GP WELDS AND 20% OF SP WELDS.
 - MAGNETIC PARTICLE EXAMINATION TO BE PERFORMED ON 1% OF GP WELDS AND 5% OF SP WELDS.
 - RADIOGRAPHY OR ULTRASONIC TESTING TO BE PERFORMED ON 2.5% FILLET WELDS AND 10% OF BUTT WELDS.
11. THE FABRICATION AND ERECTION OF THE STRUCTURAL STEELWORK TO BE SUPERVISED BY AN ENGINEER EXPERIENCED IN SUCH SUPERVISION TO ENSURE THAT ALL REQUIREMENTS OF THE DESIGN ARE MET.
12. THE CONTRACTOR TO PROVIDE ALL CLEATS AND DRILL ALL HOLES NECESSARY FOR FIXING STEEL ELEMENTS WHETHER OR NOT DETAILED ON THE DRAWINGS.
13. SUITABLE EQUIPMENT TO BE USED DURING LOADING, TRANSPORT AND ERECTION OF STEELWORK TO AVOID DAMAGE TO THE STEELWORK FINISHES. STEELWORK STORED ON SITE TO BE PROTECTED AGAINST CORROSION OR DETERIORATION OF PAINTED SURFACES.
14. AFTER TIGHTENING, EXPOSED FACES OF BOLTS, NUTS AND WASHERS SHALL BE PREPARED AND COATED AS SPECIFIED OR AS FOR ADJACENT STEELWORK.
15. THE ENDS OF ALL HOLLOW SECTIONS SHALL BE SEALED.
16. ALL COLD FORMED SECTIONS TO CONFORM TO AS 1538 AND SHALL BE ROLL-FORMED FROM ZINC COATED HIGH STRENGTH STEEL STRIP, ZINC-HIGH-TEN MINIMUM YIELD STRESS 450 MPa, 300 g/m² MINIMUM COATING MASS UNLESS OTHERWISE NOTED ON DRAWINGS.
ALL PURLINS, GIRTS AND BRIDGING TO BE LYSAGHT OR APPROVED EQUIVALENT.
17. ALL CASES OF DAMAGE TO THE PROTECTIVE COATING OF STEELWORK SHALL BE BROUGHT TO THE ATTENTION OF THE ENGINEER. WITH THE ENGINEER'S APPROVAL, MINOR DAMAGE MAY BE REPAIRED AS FOLLOWS:-
MECHANICALLY GRIND SURFACE TO ACHIEVE SMOOTH AND BRIGHT METAL COMPARABLE TO CLASS 2½.
APPLY ZINC RICH PRIMER TO A DRY FILM THICKNESS AS PER SPECIFICATION REQUIREMENTS.
18. ABBREVIATIONS
CFW - CONTINUOUS FILLET WELD
FSBW - FULL PENETRATION BUTT WELD
PPBW - PARTIAL PENETRATION BUTT WELD
19. THE LOCATION OF ALL EXISTING ELEMENTS SHALL BE SITE MEASURED PRIOR TO THE PREPARATION OF SHOP DRAWINGS.
20. ALL REACTIONS SHOWN ARE IN KN U.N.O.

					CORDOR Pty. Limited TIA ALDRED WU & ASSOCIATES PO BOX 133 KILLARA, NSW 2071 M: 041139 899 a@redwu@gmail.com					1. THIS DRAWING IS THE COPYRIGHT OF NASTASI & ASSOCIATES CONSULTING CIVIL & STRUCTURAL ENGINEERS, UNIT 5, 1-3 Whyalla Place,Prestons, 2170. PO Box 6048, Hammondville, NSW, 2170. 2. IT IS NOT ALLOWED TO COPY OR REPRODUCE ITS CONTENTS IN ANY FORM EXCEPT FOR THE PURPOSE, WHICH IT IS ISSUED WITHOUT THE NECESSITY OF OBTAINING THE AUTHORITY OF THE ISSUING AUTHORITY. 3. DO NOT SCALE THIS DRAWING, ONLY STATED DIMENSIONS ARE TO BE CONSIDERED. 4. CONTRACTOR TO VERIFY THE DETAIL / INFORMATION GIVEN IN THIS DRAWING, ANY DISCREPANCIES SHALL BE BROUGHT TO ENGINEERS ATTENTION PRIOR TO COMMENCEMENT OF WORK, FAILURE TO COMPLY WITH THE ABOVE WILL BE CONTRACTORS LIABILITY.  NASTASI & ASSOCIATES CONSULTING ENGINEERS RESIDENTIAL - COMMERCIAL - INDUSTRIAL - INFRASTRUCTURE STRUCTURAL - CIVIL - STORMWATER - GEOTECHNICAL - SURVEYING - SITE SERVICES OPERATING IN - NSW - QLD - VIC - TAS Head Office: Unit 5, 1-3 Whyalla Place, Prestons, NSW 2170 www.nastasiassociates.com.au ABN : 45 533 226 008 Ph (02) 96072864 QUALITY CONTROL DRAWN C.L. 19.05.2023 DESIGNED DATE R.N. 19.05.2023 CHECKED DATE APPROVED:  S. NASTASI B.E.,M.I.E. AUST, CPENG CLIENT: PROJECT: 83 BRIXTON ROAD, BERALA NSW 2141 TITLE: GENERAL NOTES SHEET 2 DRAWING STATUS ISSUED FOR CONSTRUCTION SCALE (AT ORIGINAL SIZE) AS NOTED PROJECT NO. DRAWING NO. REVISION NO. 31734 S00.01 A <tr><td colspan="5"></td><td colspan="5"></td><td Approved Construction Certificate
F2022-/00093
Issued By First Building Certifiers P/L BDC 3219

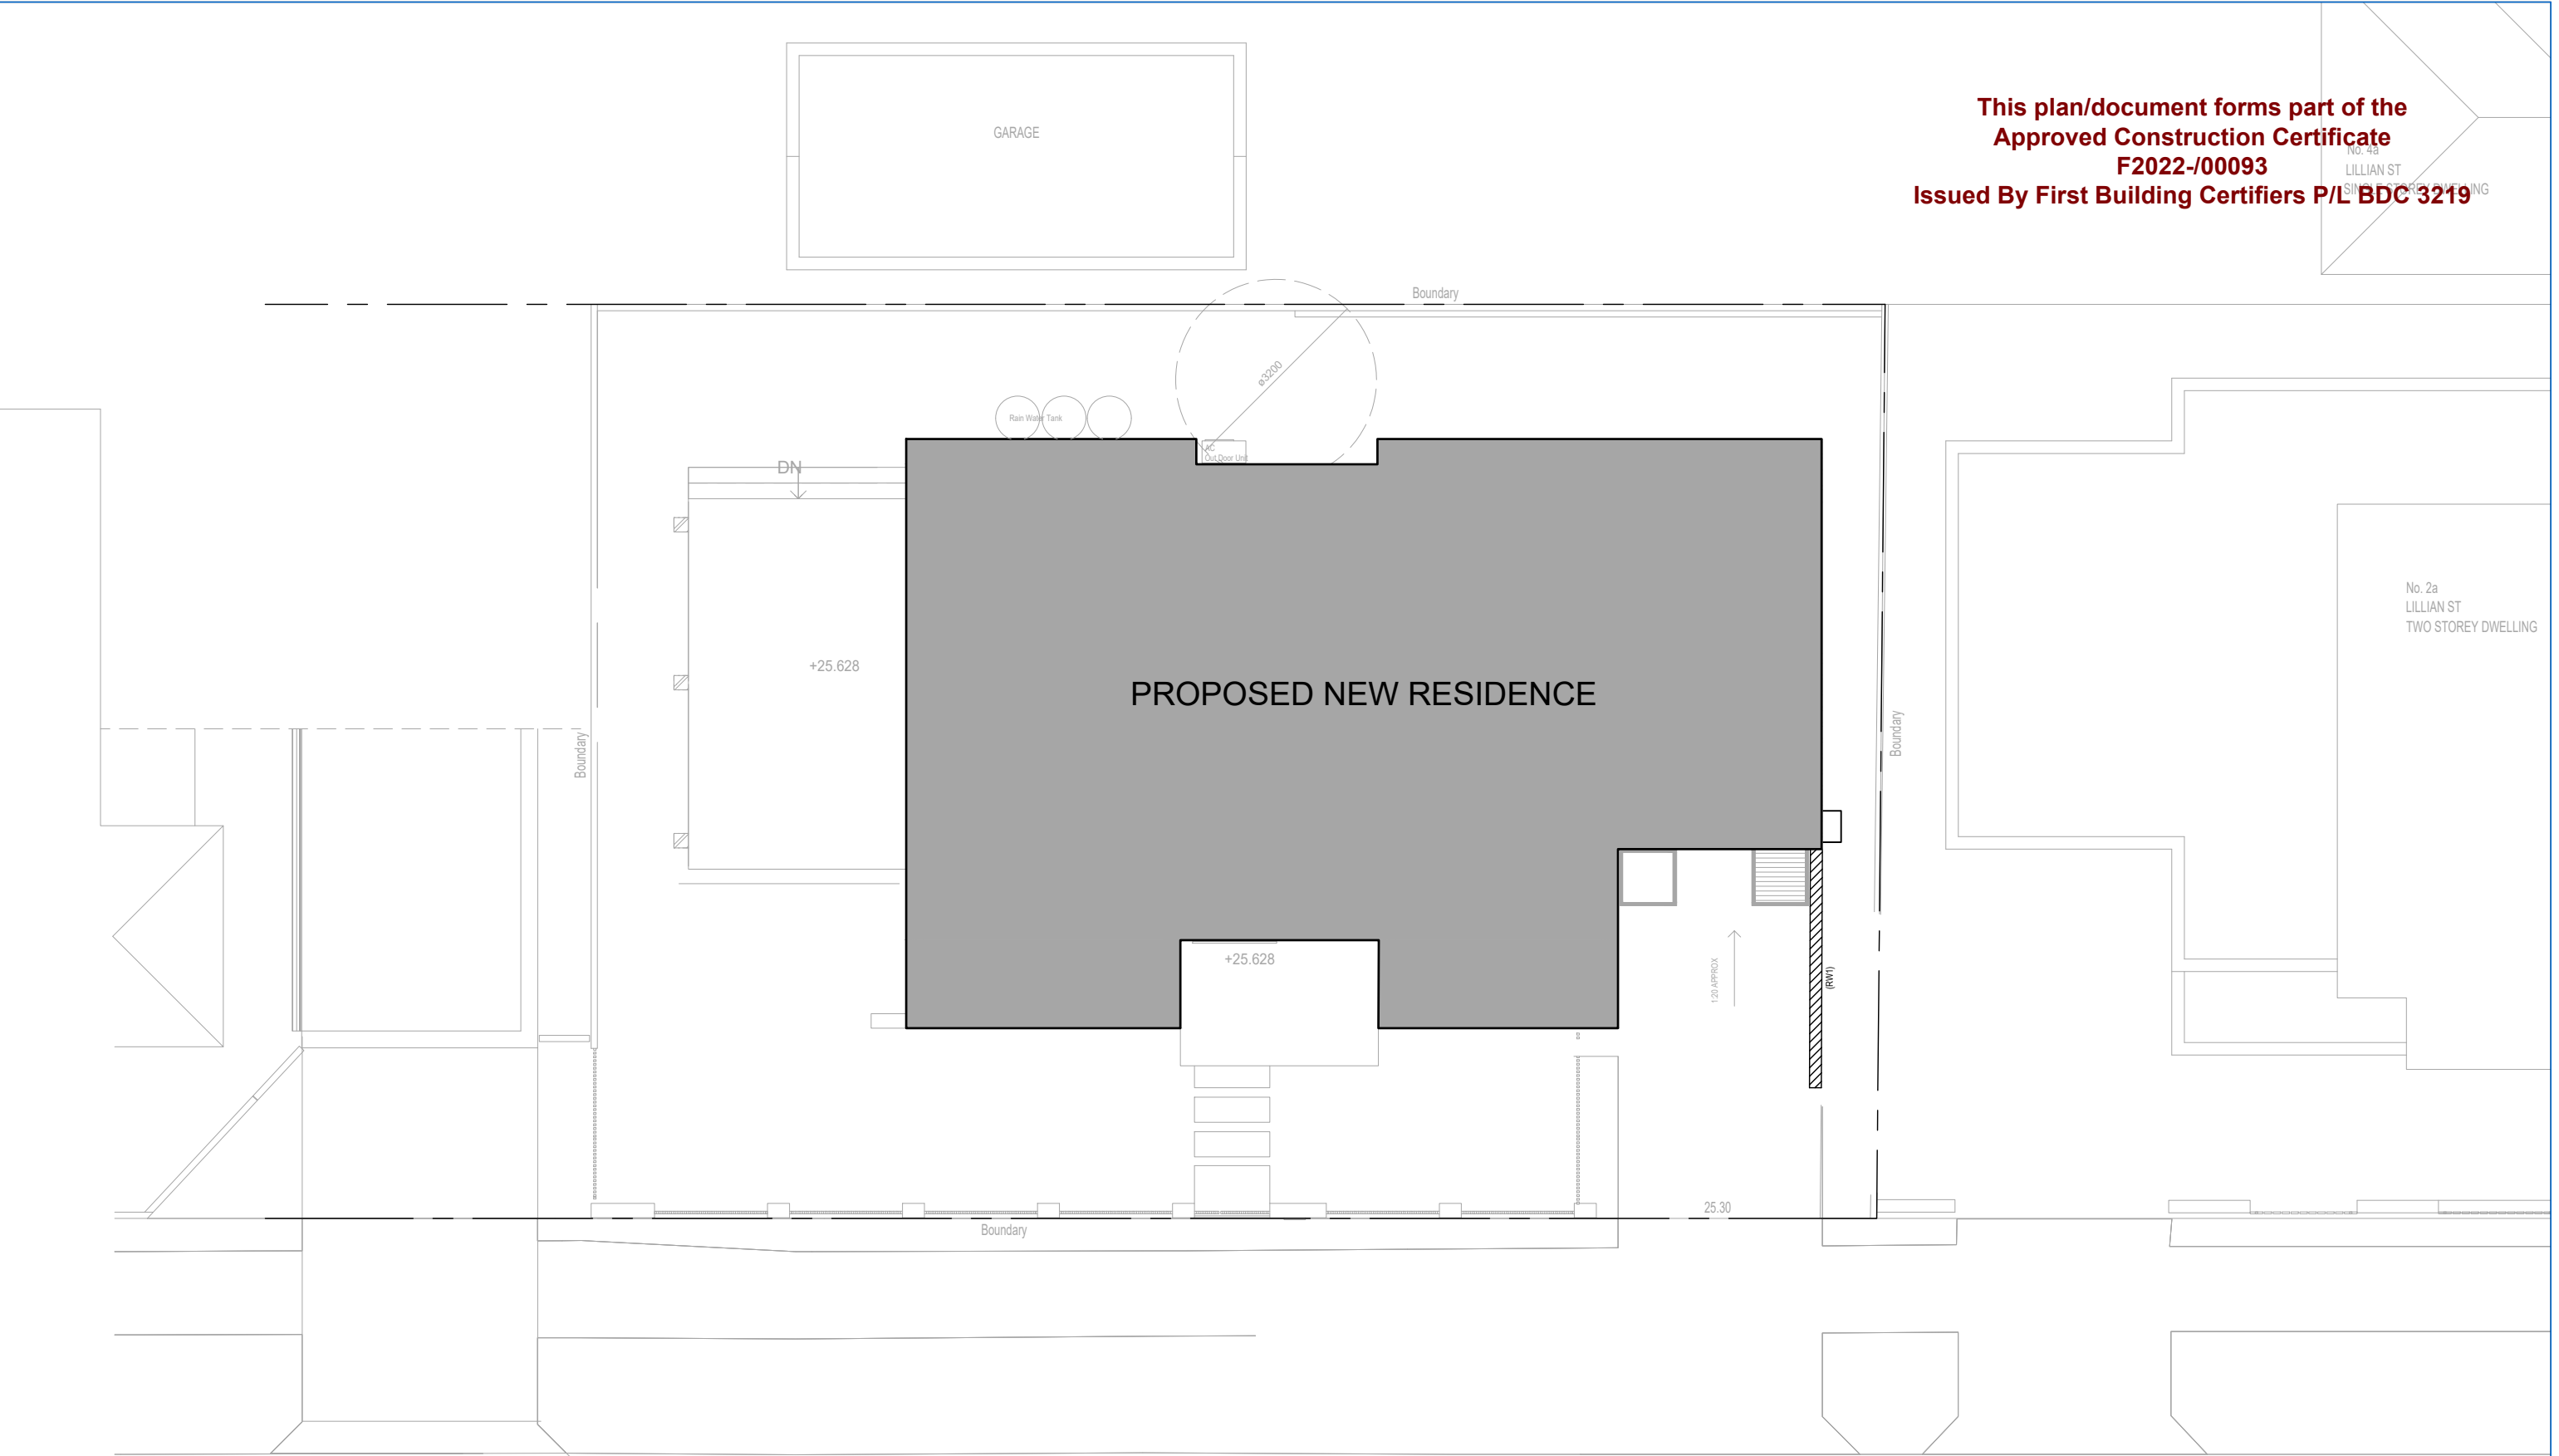


EXTERNAL WORKS PLAN
SCALE 1:200

HYDE PARK ROAD

LEGEND:
(RW1) - DENOTES 190 RETAINING WALL (REFER TO DETAIL ON S01.10)

				CORDOR Pty. Limited T/A ALDRED WU & ASSOCIATES PO BOX 133 KILLARA, NSW 2071 M: 0411139 899 aldredwu@gmail.com		1. THIS DRAWING IS THE COPYRIGHT OF NASTASI & ASSOCIATES CONSULTING CIVIL & STRUCTURAL ENGINEERS, Unit 5,1-3 Whyalla Place,Prestons, 2170. PO Box 6048, Hammondville, NSW, 2170. 2. IT IS NOT ALLOWED TO COPY OR REPRODUCE IT'S CONTENTS IN ANY FORM EXCEPT FOR THE PURPOSE, WHICH IT IS INTENDED WITHOUT THE ABOVE CONSULTANT'S AUTHORITY. 3. DO NOT SCALE THIS DRAWING, ONLY STATED DIMENSIONS ARE TO BE CONSIDERED. 4. CONTRACTOR TO VERIFY THE DETAIL / INFORMATION GIVEN IN THIS DRAWING, ANY DISCREPANCIES SHALL BE BROUGHT TO ENGINEERS ATTENTION PRIOR TO COMMENCEMENT OF WORK, FAILURE TO COMPLY WITH THE ABOVE WILL BE CONTRACTORS LIABILITY.		NASTASI & ASSOCIATES CONSULTING ENGINEERS RESIDENTIAL - COMMERCIAL - INDUSTRIAL - INFRASTRUCTURE STRUCTURAL - CIVIL - STORMWATER - GEOTECHNICAL - SURVEYING - SITE SERVICES OPERATING IN - NSW - QLD - VIC - TAS Head Office: Unit 5, 1-3 Whyalla Place, Prestons, NSW 2170 www.nastasiassociates.com.au ABN - 45 533 226 008 Ph (02) 96072864		QUALITY CONTROL <table><tr><td>DRAWN</td><td>DATE</td></tr><tr><td>C.L.</td><td>19.05.2023</td></tr><tr><td>DESIGNED</td><td>DATE</td></tr><tr><td>R.N.</td><td>19.05.2023</td></tr><tr><td>CHECKED</td><td>DATE</td></tr></table>		DRAWN	DATE	C.L.	19.05.2023	DESIGNED	DATE	R.N.	19.05.2023	CHECKED	DATE	APPROVED:  S. NASTASI B.E.,M.I.E. AUST, CPENG		CLIENT: PROJECT: 83 BRIXTON ROAD, BERALA NSW 2141		TITLE: EXTERNAL WORKS		DRAWING STATUS ISSUED FOR CONSTRUCTION SCALE (AT ORIGINAL SIZE) AS NOTED <table><tr><td>PROJECT NO.</td><td>DRAWING NO.</td><td>REVISION NO.</td></tr><tr><td>31734</td><td>S01.00</td><td>A</td></tr></table>			PROJECT NO.	DRAWING NO.	REVISION NO.	31734	S01.00	A
DRAWN	DATE																																			
C.L.	19.05.2023																																			
DESIGNED	DATE																																			
R.N.	19.05.2023																																			
CHECKED	DATE																																			
PROJECT NO.	DRAWING NO.	REVISION NO.																																		
31734	S01.00	A																																		
A	19.05.23	C.L.	R.N.	ISSUED FOR CONSTRUCTION																																
Rev.	Date	Drawn	Eng	Description																																


**This plan/document forms part of the
Approved Construction Certificate
F2022-/00093
Issued By First Building Certifiers P/L BDC 3219**

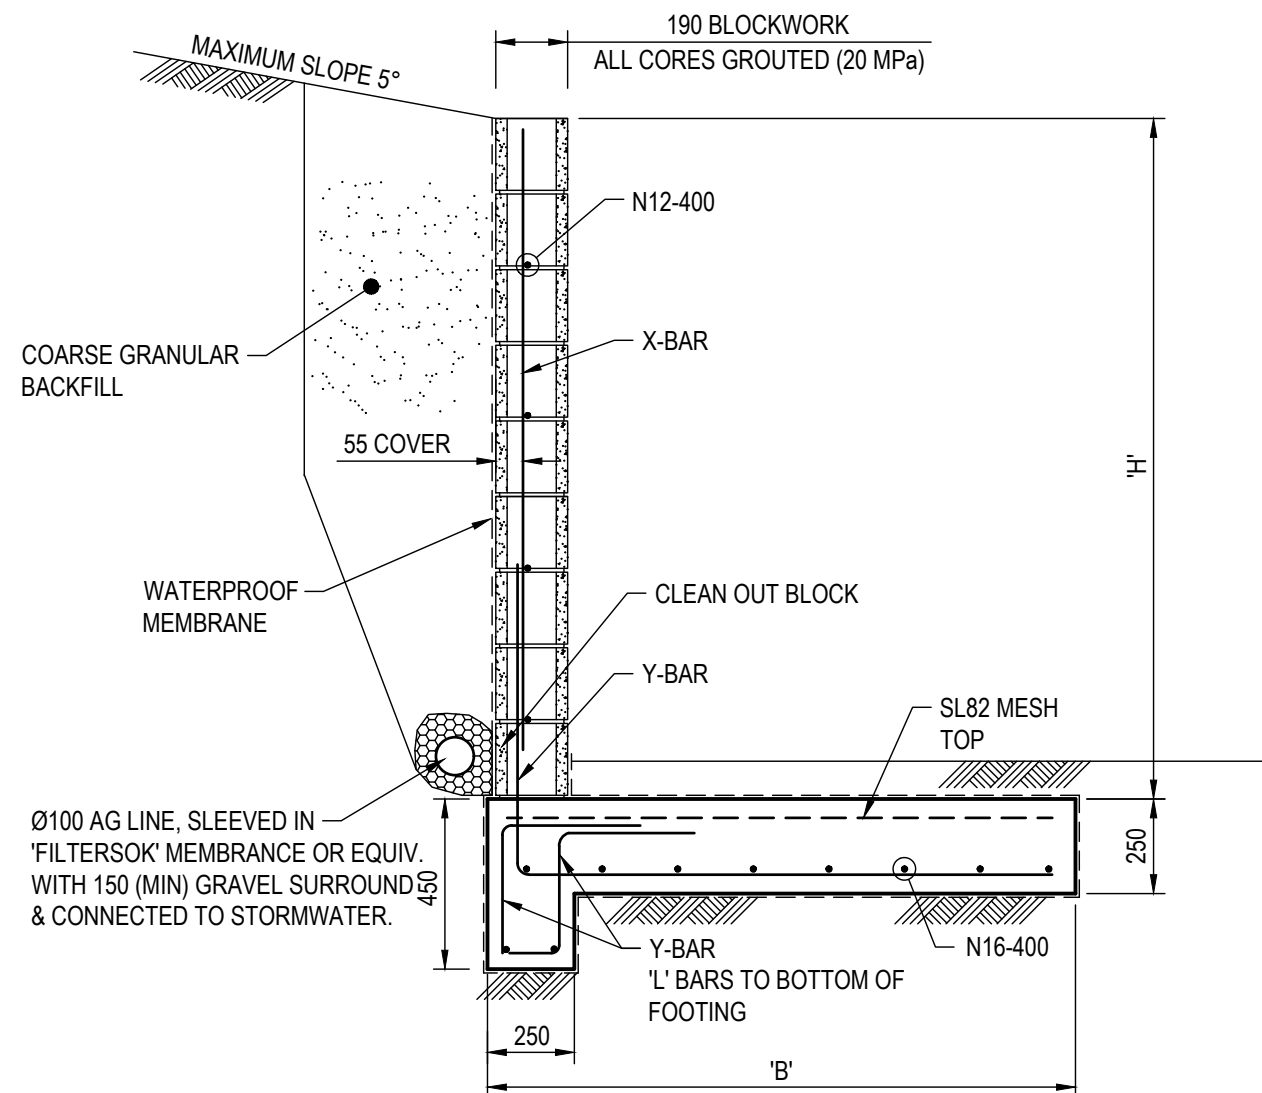

TYPICAL BLOCK RETAINING WALL DETAIL RW1

SCALE 1:20

HEIGHT 'H' (mm)	600	1000	1400	1800
REINFORCEMENT 'Y' & 'X'	N12-400CTS	N12-400CTS	N16-400CTS	N16-400CTS
BASE WIDTH 'B'	450	900	1100	1400

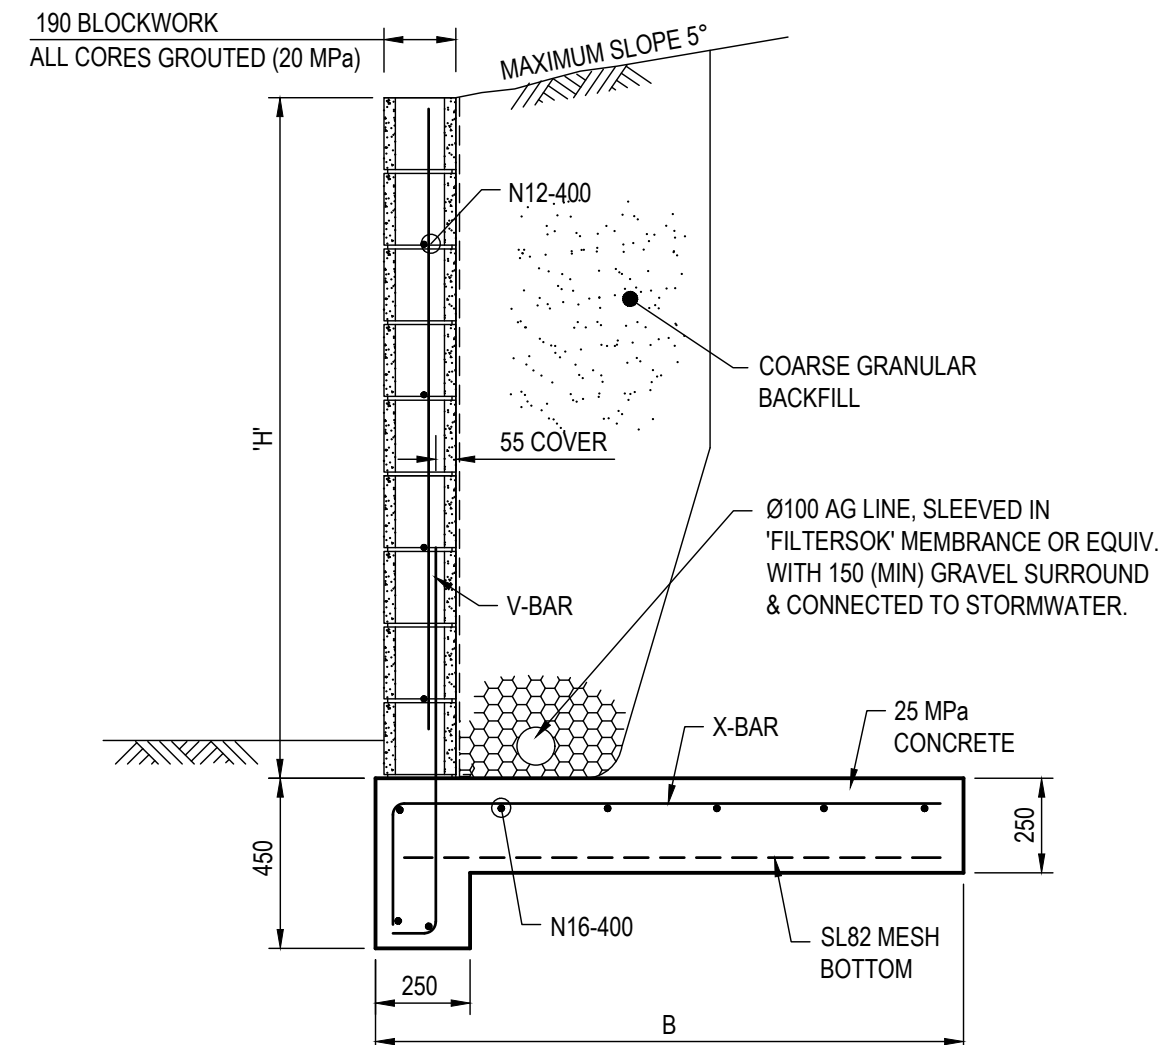


ALTERNATE BLOCK RETAINING WALL DETAIL 'RW1'

SCALE 1:20

HEIGHT 'H' (mm)	600	1000	1400	1800
REINFORCEMENT 'V' & 'X'	N12-600CTS	N12-400CTS	N16-400CTS	N16-400CTS
BASE WIDTH 'B'	450	900	1100	1400

				CORDOR Pty. Limited TIA ALDRED WU & ASSOCIATES PO BOX 133 KILLARA, NSW 2071 M: 0411139 899 aldredwu@gmail.com		1. THIS DRAWING IS THE COPYRIGHT OF NASTASI & ASSOCIATES CONSULTING CIVIL & STRUCTURAL ENGINEERS, Unit 5-1-3 Whyalla Place, Prestons, 2170. PO Box 6046, Hammondville, NSW, 2170. 2. IT IS NOT ALLOWED TO COPY OR REPRODUCE ITS CONTENTS IN ANY FORM EXCEPT FOR THE PURPOSE WHICH IT IS INTENDED WITHOUT THE ABOVE CONSULTANT'S AUTHORITY. 3. DO NOT SCALE THIS DRAWING. ONLY STATED DIMENSIONS ARE TO BE CONSIDERED. 4. CONTRACTOR TO VERIFY THE DETAIL / INFORMATION GIVEN IN THIS DRAWING. ANY DISCREPANCIES SHALL BE BROUGHT TO ENGINEERS ATTENTION PRIOR TO COMMENCEMENT OF WORK. FAILURE TO COMPLY WITH THE ABOVE WILL BE CONTRACTORS LIABILITY.		NASTASI & ASSOCIATES CONSULTING ENGINEERS RESIDENTIAL - COMMERCIAL - INDUSTRIAL - INFRASTRUCTURE STRUCTURAL - CIVIL - STORMWATER - GEOTECHNICAL - SURVEYING - SITE SERVICES OPERATING IN - NSW - QLD - VIC - TAS Head Office: Unit 5, 1-3 Whyalla Place, Prestons, NSW 2170 www.nastasiassociates.com.au ABN - 45 533 225 006 Ph (02) 96072864		QUALITY CONTROL <table><tr><td>DRAWN</td><td>DATE</td></tr><tr><td>C.L.</td><td>19.05.2023</td></tr><tr><td>DESIGNED</td><td>DATE</td></tr><tr><td>R.N.</td><td>19.05.2023</td></tr><tr><td>CHECKED</td><td>DATE</td></tr></table>		DRAWN	DATE	C.L.	19.05.2023	DESIGNED	DATE	R.N.	19.05.2023	CHECKED	DATE	APPROVED:  S. NASTASI B.E.M.I.E. AUST. CPENG		CLIENT: PROJECT: 83 BRIXTON ROAD, BERALA NSW 2141		TITLE: EXTERNAL WORKS DETAILS - SHEET 1		DRAWING STATUS ISSUED FOR CONSTRUCTION SCALE (AT ORIGINAL SIZE)AS NOTED <table><tr><td>PROJECT NO.</td><td>DRAWING NO.</td><td>REVISION NO.</td></tr><tr><td>31734</td><td>S01.10</td><td>A</td></tr></table>		PROJECT NO.	DRAWING NO.	REVISION NO.	31734	S01.10	A
DRAWN	DATE																																		
C.L.	19.05.2023																																		
DESIGNED	DATE																																		
R.N.	19.05.2023																																		
CHECKED	DATE																																		
PROJECT NO.	DRAWING NO.	REVISION NO.																																	
31734	S01.10	A																																	
A	19.05.23	C.L.	R.N.	ISSUED FOR CONSTRUCTION																															
Rev.	Date	Drawn	Eng	Description																															

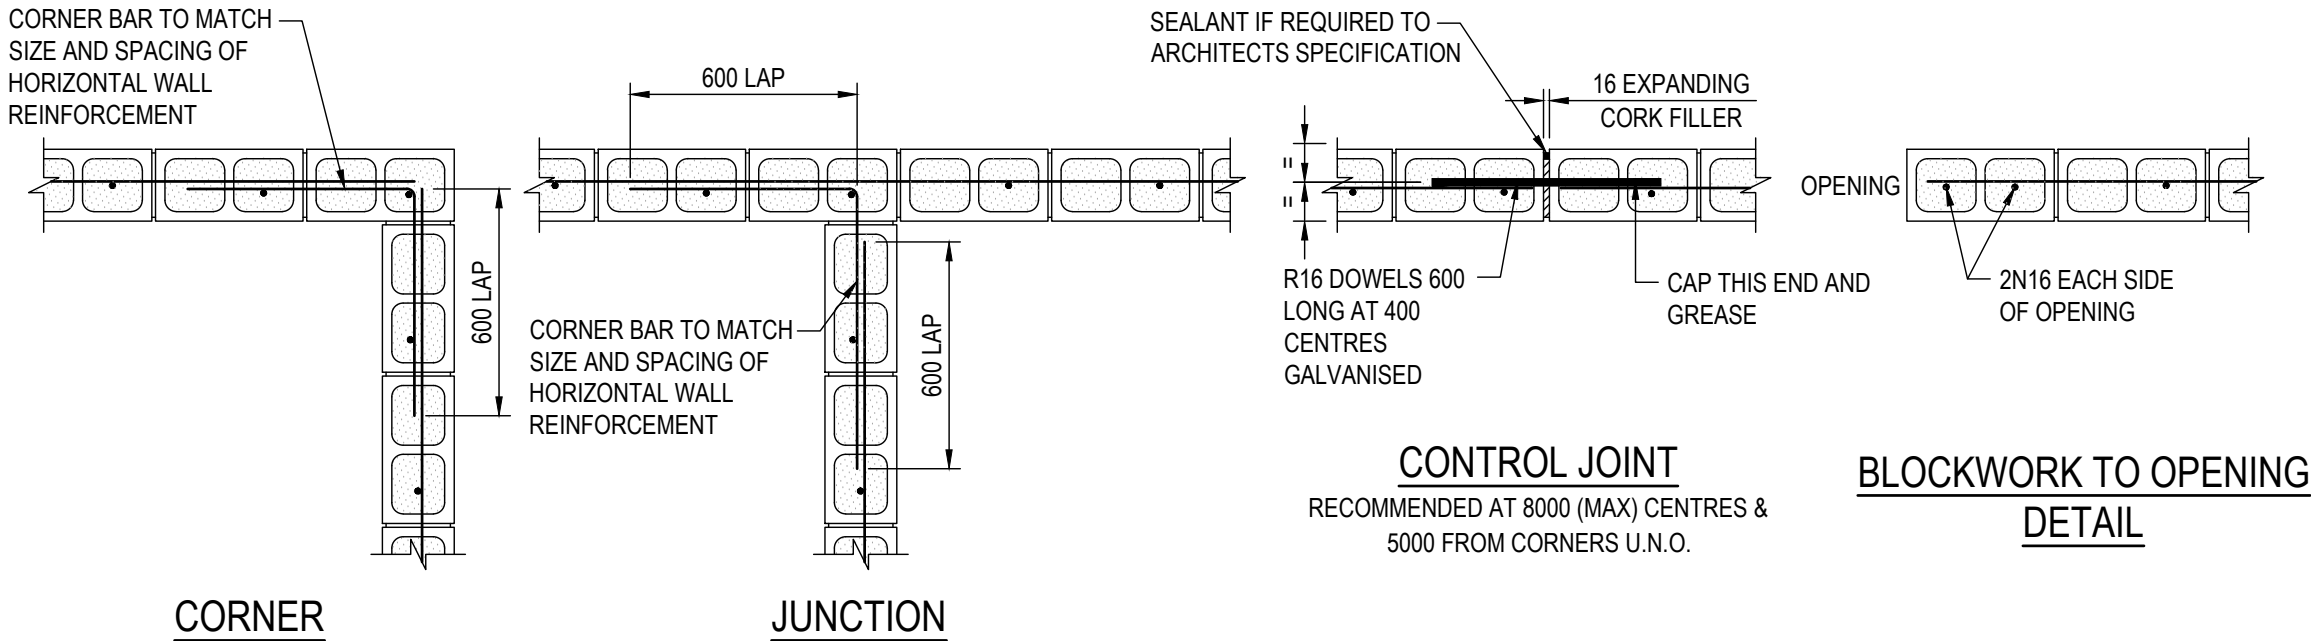

TYPICAL REINFORCED BLOCKWALL PLANS

CONTROL JOINTS TO BE VERTICAL FOR FULL HEIGHT OF WALL.
APPLY SEALANTS AS SPECIFIED TO EACH FACE OF BLOCKWALL.

				CORDOR Pty. Limited TIA ALDRED WU & ASSOCIATES PO BOX 133 KILLARA, NSW 2071 M: 0411139 899 aldredwu@gmail.com	NASTASI & ASSOCIATES CONSULTING ENGINEERS RESIDENTIAL - COMMERCIAL - INDUSTRIAL - INFRASTRUCTURE STRUCTURAL - CIVIL - STORMWATER - GEOTECHNICAL - SURVEYING - SITE SERVICES OPERATING IN - NSW - QLD - VIC - TAS Head Office: Unit 5, 1-3 Whyalla Place, Prestons, NSW 2170 www.nastasiassociates.com.au ABN: 45 533 226 008 Ph (02) 96072864	QUALITY CONTROL DRAWN DATE C.L. 19.05.2023 DESIGNED DATE R.N. 19.05.2023 CHECKED DATE	APPROVED: S. NASTASI B.E., M.I.E. AUST., CPENG	CLIENT: PROJECT: 83 BRIXTON ROAD, BERALA NSW 2141	TITLE: EXTERNAL WORKS DETAILS - SHEET 2	DRAWING STATUS ISSUED FOR CONSTRUCTION SCALE (AT ORIGINAL SIZE) AS NOTED PROJECT NO. DRAWING NO. REVISION NO. 31734 S01.10 A		
A	19.05.23	C.L.	R.N.				ISSUED FOR CONSTRUCTION					
Rev.	Date	Drawn	Eng				Description					

[illegible]

SCALE 1:100


LEGEND:

 - DENOTES Ø500 MASS CONCRETE PILE.
FOUNDED ON ROCK WITH MINIMUM
ALLOWABLE BEARING CAPACITY 700 KPa
MIN. 3000 DEEP

NOTE:
SEWER'S LOCATION IS SHOWN
APPROXIMATE. BUILDER TO
CONFIRM SEWER'S LOCATION
PRIOR TO CONSTRUCTION.

					CORDOR Pty. Limited TIA ALDRED WU & ASSOCIATES PO BOX 133 KILLARA, NSW 2071 M: 0411133 899 aldredwu@gmail.com		1. THIS DRAWING IS THE COPYRIGHT OF NASTASI & ASSOCIATES CONSULTING CIVIL & STRUCTURAL ENGINEERS, Unit 5,1-3 Whyalla Place,Prestons, 2170, PO Box 6545, HARRISBURG, NSW, 2170. 2. IT IS NOT ALLOWED TO COPY OR REPRODUCE ITS CONTENTS IN ANY FORM EXCEPT FOR THE PURPOSE, WHICH IT IS INTENDED WITHOUT THE ABOVE CONSULTANT'S AUTHORITY. 3. DO NOT SCALE THIS DRAWING, ONLY STATED DIMENSIONS ARE TO BE CONSIDERED. 4. CONTRACTOR TO VERIFY THE DETAIL / INFORMATION GIVEN IN THIS DRAWING, ANY DISCREPANCIES SHALL BE BROUGHT TO ENGINEERS ATTENTION PRIOR TO COMMENCEMENT OF WORK, FAILURE TO COMPLY WITH THE ABOVE WILL BE CONTRACTORS LIABILITY.		NASTASI & ASSOCIATES CONSULTING ENGINEERS RESIDENTIAL - COMMERCIAL - INDUSTRIAL - INFRASTRUCTURE STRUCTURAL - CIVIL - STORMWATER - GEOTECHNICAL - SURVEYING - SITE SERVICES OPERATING IN - NSW - QLD - VIC - TAS Head Office: Unit 5, 1-3 Whyalla Place, Prestons, NSW 2170 www.nastasiassociates.com.au ABN : 45 533 226 008 Ph (02) 96072864		QUALITY CONTROL DRAWNDATE C.L.19.05.2023 DESIGNEDDATE R.N.19.05.2023 CHECKEDDATE		APPROVED:  S. NASTASI B.E.,M.I.E. AUST, CPENG		CLIENT: PROJECT: 83 BRIXTON ROAD, BERALA NSW 2141		TITLE: FOOTING PLAN		DRAWING STATUS ISSUED FOR CONSTRUCTION SCALE (AT ORIGINAL SIZE)AS NOTED PROJECT NO. DRAWING NO. REVISION NO. 31734S02.00A	
A19.05.23C.L.R.N.ISSUED FOR CONSTRUCTION Rev. Date Drawn Eno Description																				

This plan/document forms part of the
Approved Construction Certificate
F2022-/00093
Issued By First Building Certifiers P/L BDC 3219

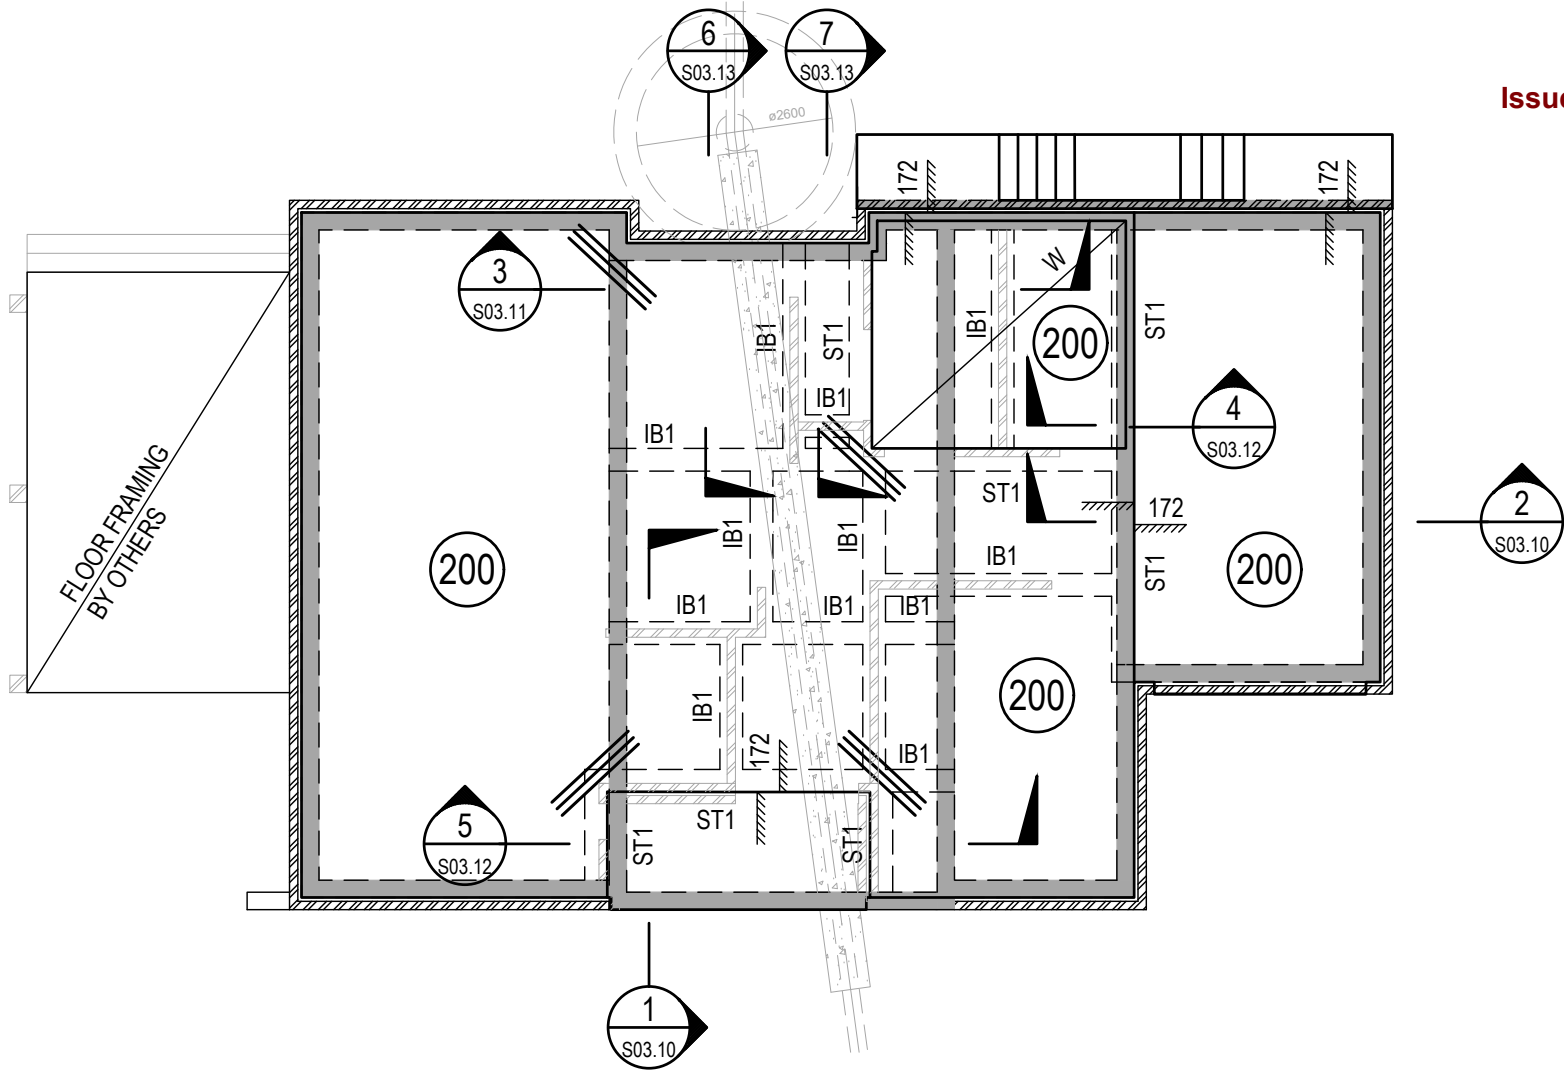

NOTE:
ALL LOAD BEARING BRICKWORK
TO BE 15MPa STRUCTURAL
GRADE SOLID BRICKS.

GROUND FLOOR SLAB PLAN

SCALE 1:100

NOTES:

200


- DENOTES CONCRETE SLAB THICKNESS.
SL102 MESH TOP
SL102 MESH BOTTOM

IB1


- DENOTES INTERNAL BEAM.
(REFER TO TYPICAL DETAIL)

ST1

- DENOTES STEP BEAM.
(REFER TO TYPICAL DETAIL)

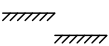

- DENOTES SLAB STEP

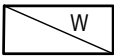

- DENOTES 50mm WET AREA SET DOWN.



- DENOTES LOAD BEARING WALL UNDER



- DENOTES 3-N12 TRIMMING BARS(TOP)
2000 LONG

A	19.05.23	C.L.	R.N.	ISSUED FOR CONSTRUCTION	
Rev.	Date	Drawn	Eng	Description	

CORDOR Pty. Limited

T/A ALDRED WU & ASSOCIATES

PO BOX 133
KILLARA, NSW 2071
M: 0411139 899
aldredwu@gmail.com

1. THIS DRAWING IS THE COPYRIGHT OF NASTASI & ASSOCIATES CONSULTING CIVIL & STRUCTURAL ENGINEERS, Unit 5, 1-3 Whyalla Place, Prestons, 2170. PO Box 6048, Hammondville, NSW, 2170.
2. IT IS NOT ALLOWED TO COPY OR REPRODUCE IT'S CONTENTS IN ANY FORM EXCEPT FOR THE PURPOSE, WHICH IT IS INTENDED WITHOUT THE ABOVE CONSULTANT'S AUTHORITY.
3. DO NOT SCALE THIS DRAWING, ONLY STATED DIMENSIONS ARE TO BE CONSIDERED.
4. CONTRACTOR TO VERIFY THE DETAIL / INFORMATION GIVEN IN THIS DRAWING, ANY DISCREPANCIES SHALL BE BROUGHT TO ENGINEERS ATTENTION PRIOR TO COMMENCEMENT OF WORK, FAILURE TO COMPLY WITH THE ABOVE WILL BE CONTRACTORS LIABILITY.

NASTASI & ASSOCIATES
CONSULTING ENGINEERS

RESIDENTIAL - COMMERCIAL - INDUSTRIAL - INFRASTRUCTURE
STRUCTURAL - CIVIL - STORMWATER - GEOTECHNICAL - SURVEYING - SITE SERVICES
OPERATING IN - NSW - QLD - VIC - TAS

Head Office: Unit 5, 1-3 Whyalla Place, Prestons, NSW 2170
www.nastasiassociates.com.au
ABN - 45 533 226 008
Ph (02) 96072864

QUALITY CONTROL

DRAWN	DATE
C.L.	19.05.2023
DESIGNED	DATE
R.N.	19.05.2023
CHECKED	DATE

APPROVED:


S. NASTASI
B.E., M.I.E. AUST, CPENG

CLIENT:

PROJECT:

83 BRIXTON ROAD,
BERALA NSW 2141

TITLE:

GROUND FLOOR
SLAB PLAN

DRAWING STATUS


ISSUED FOR CONSTRUCTION

SCALE (AT ORIGINAL SIZE)

AS NOTED

PROJECT NO.	DRAWING NO.	REVISION NO.
31734	S03.00	A

This plan/document forms part of the
Approved Construction Certificate
F2022-/00093
Issued By First Building Certifiers P/L BDC 3219

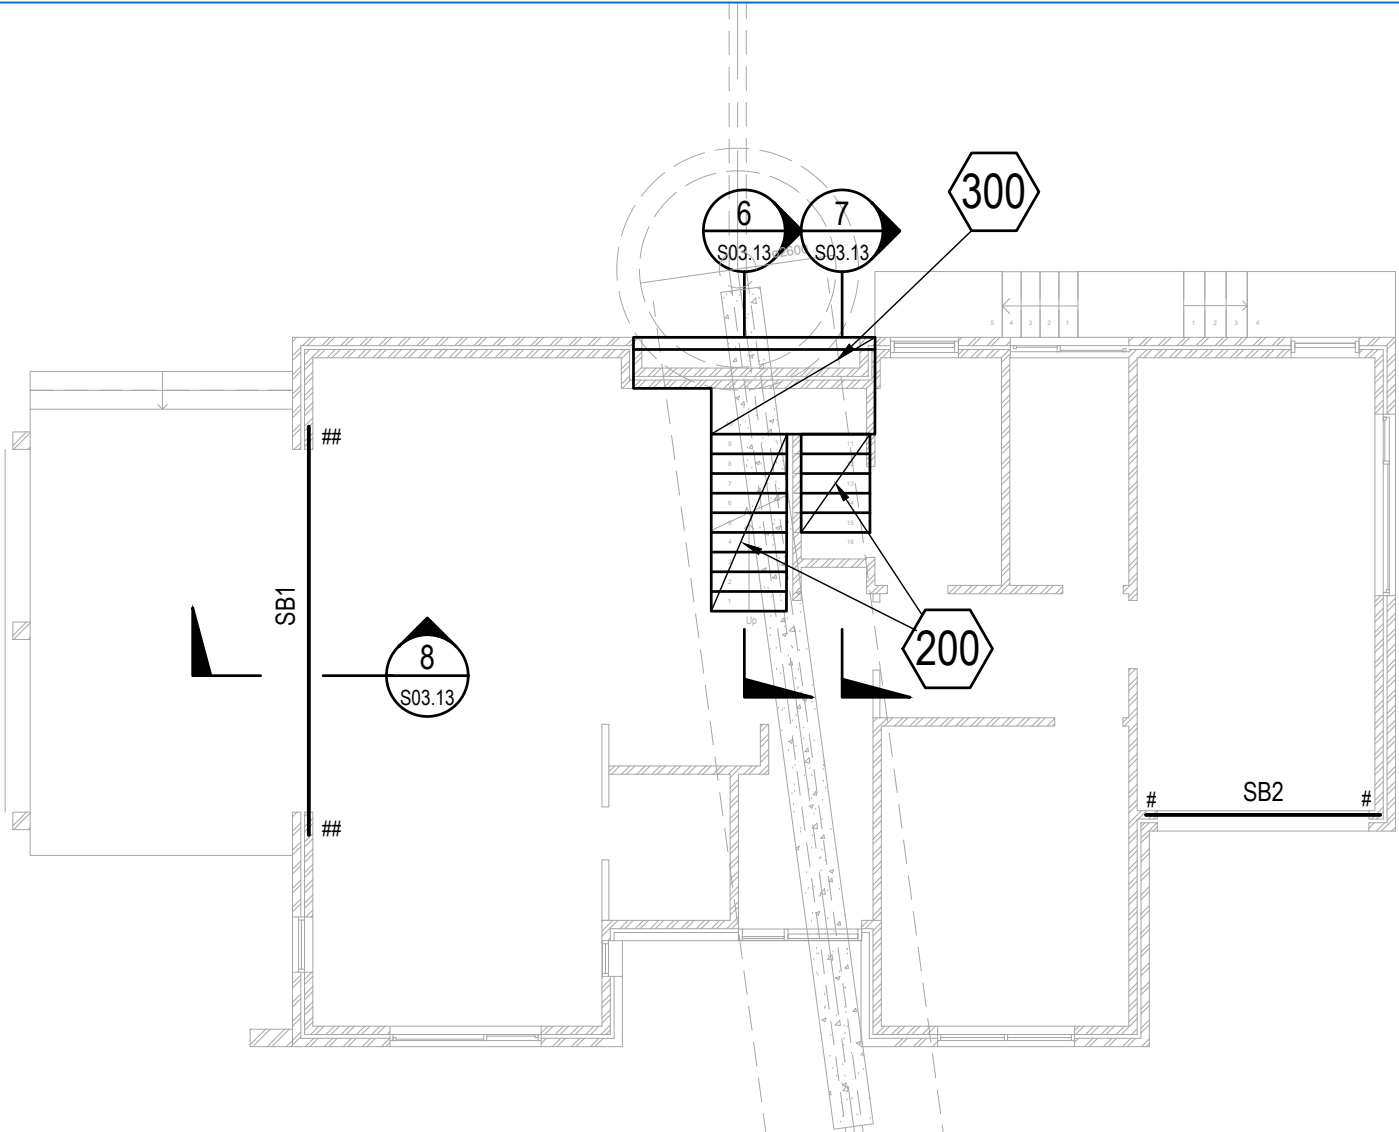

GROUND FLOOR BEAM LAYOUT & STAIR LANDING SLAB PLAN

SCALE 1:100

LEGEND:



- DENOTES 200 THICK SLAB
REINFORCED WITH N12-200 TOP & BOTTOM EACH WAY




- DENOTES 300 THICK LANDING SLAB
REINFORCED WITH N12-200 TOP & BOTTOM EACH WAY

STEEL MEMBER SCHEDULE


MARK	DESIGNATION	COMMENTS
BEAMS		
SB1	380 PFC + 10 PLATE	
SB2	200 PFC + 10 PLATE	
#	DENOTES 150 END BEARING	
##	DENOTES 300 END BEARING	
	DENOTES FLOOR JOIST SPANNING DIRECTION. MEMBER SIZE BY OTHERS.	

				CORDOR Pty. Limited T/A ALDRED WU & ASSOCIATES PO BOX 133 KILLARA, NSW 2071 M: 0411139 899 aldredwu@gmail.com		1. THIS DRAWING IS THE COPYRIGHT OF NASTASI & ASSOCIATES CONSULTING CIVIL & STRUCTURAL ENGINEERS, Unit 5,1-3 Whyalla Place,Prestons, 2170. PO Box 6048, Hammondville, NSW, 2170. 2. IT IS NOT ALLOWED TO COPY OR REPRODUCE IT'S CONTENTS IN ANY FORM EXCEPT FOR THE PURPOSE, WHICH IT IS INTENDED WITHOUT THE ABOVE CONSULTANT'S AUTHORITY. 3. DO NOT SCALE THIS DRAWING, ONLY STATED DIMENSIONS ARE TO BE CONSIDERED. 4. CONTRACTOR TO VERIFY THE DETAIL / INFORMATION GIVEN IN THIS DRAWING, ANY DISCREPANCIES SHALL BE BROUGHT TO ENGINEERS ATTENTION PRIOR TO COMMENCEMENT OF WORK, FAILURE TO COMPLY WITH THE ABOVE WILL BE CONTRACTORS LIABILITY.		NASTASI & ASSOCIATES CONSULTING ENGINEERS RESIDENTIAL - COMMERCIAL - INDUSTRIAL - INFRASTRUCTURE STRUCTURAL - CIVIL - STORMWATER - GEOTECHNICAL - SURVEYING - SITE SERVICES OPERATING IN - NSW - QLD - VIC - TAS Head Office: Unit 5, 1-3 Whyalla Place, Prestons, NSW 2170 www.nastasiassociates.com.au ABN - 45 533 226 008 Ph (02) 96072864		QUALITY CONTROL DRAWN DATE C.L. 19.05.2023 DESIGNED DATE R.N. 19.05.2023 CHECKED DATE		APPROVED:  S. NASTASI B.E.,M.I.E. AUST, CPENG		CLIENT: PROJECT: 83 BRIXTON ROAD, BERALA NSW 2141		TITLE: GROUND FLOOR BEAM & STAIR LANDING SLAB PLAN		DRAWING STATUS ISSUED FOR CONSTRUCTION SCALE (AT ORIGINAL SIZE) AS NOTED PROJECT NO. DRAWING NO. REVISION NO. 31734 S03.01 A		
A	19.05.23	C.L.	R.N.	ISSUED FOR CONSTRUCTION																
Rev.	Date	Drawn	Eng	Description																

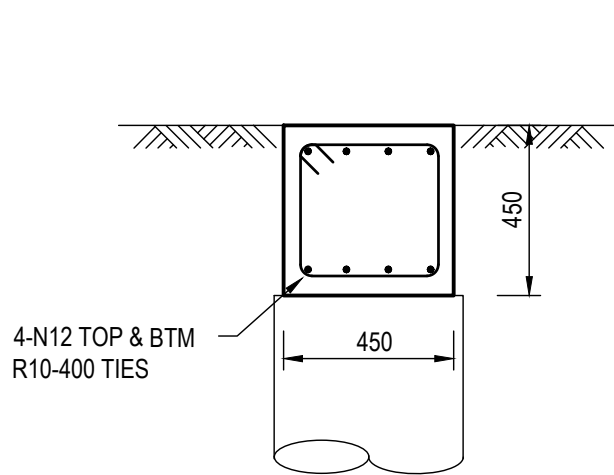



TYPICAL 'SF1' DETAIL

SCALE 1:20

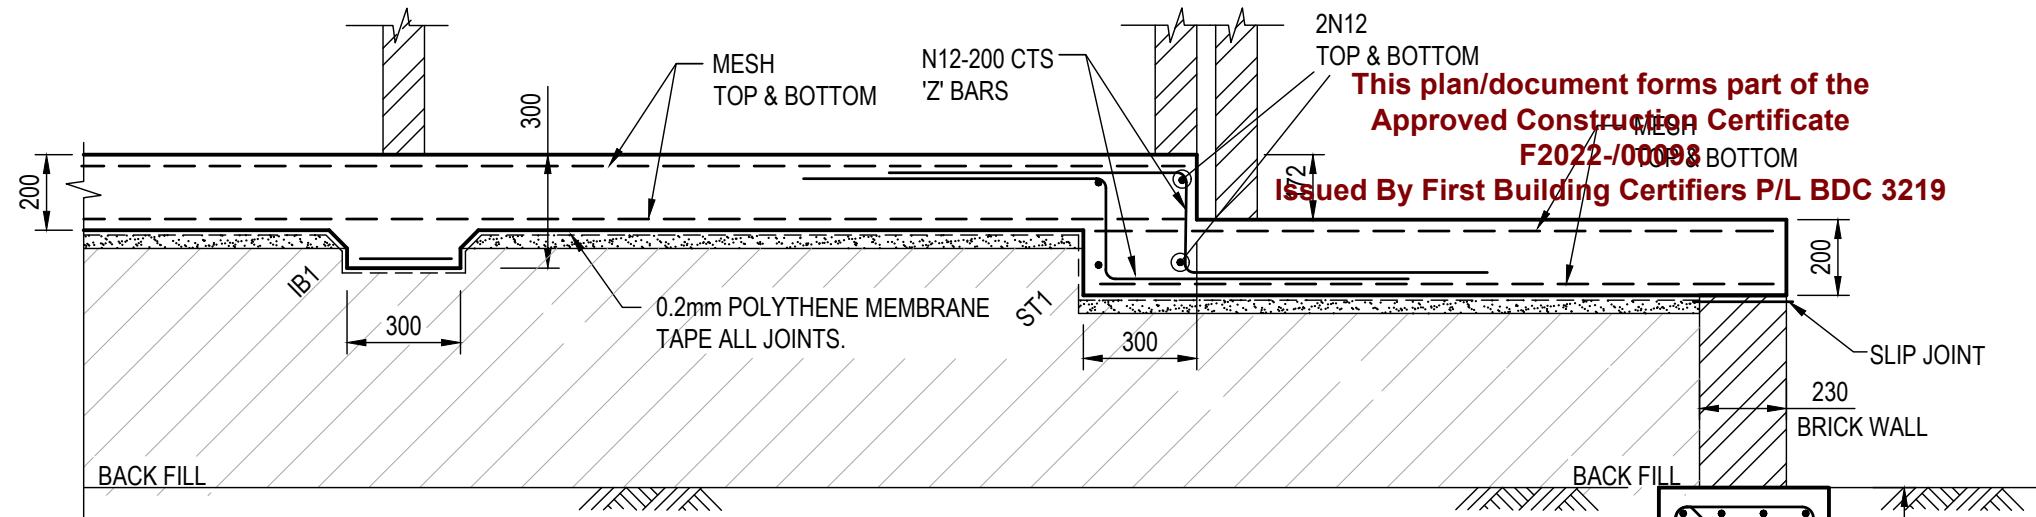


SECTION 1

SCALE 1:20

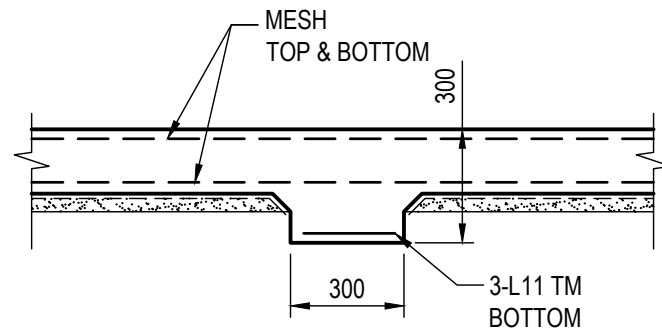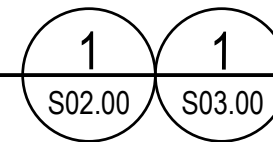


TYPICAL 'IB1' DETAIL

SCALE 1:20

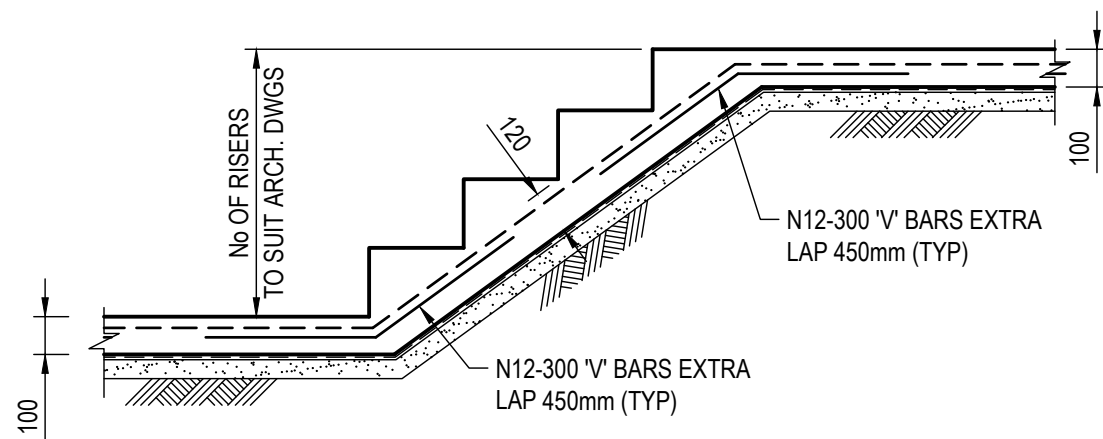


TYPICAL WALKWAY STAIRS

SCALE 1:20

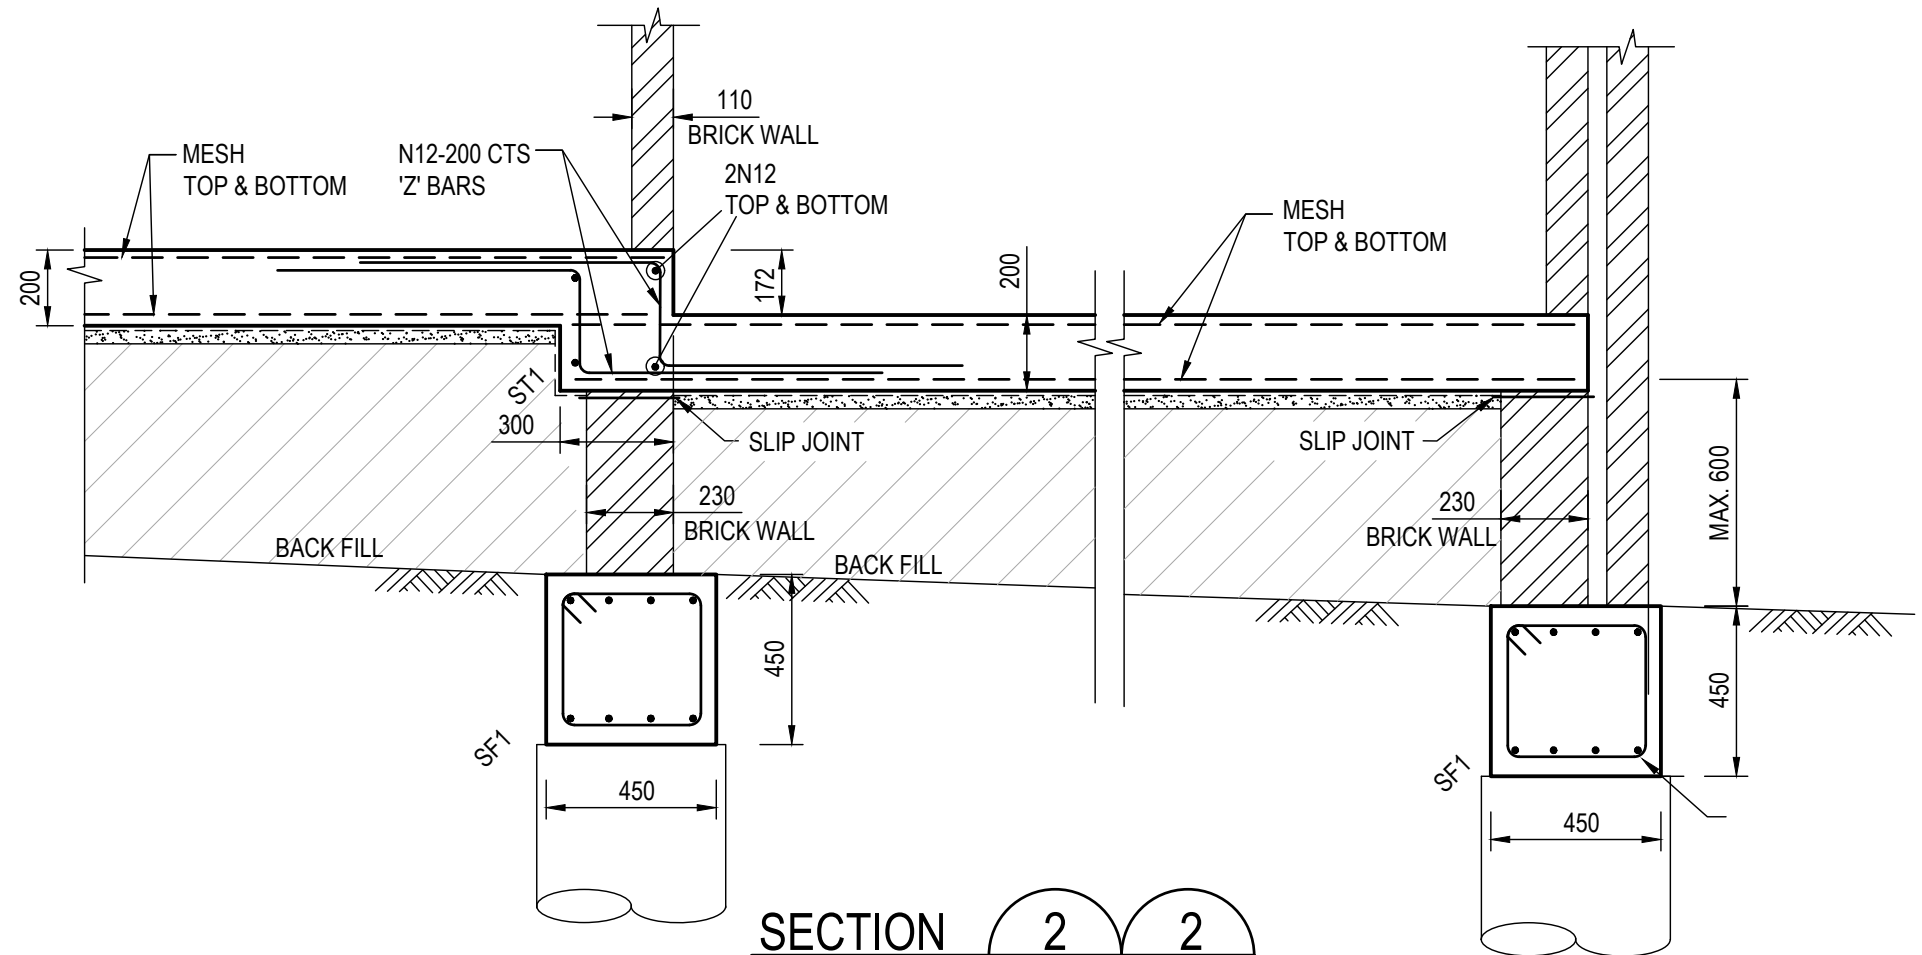

SECTION 2

SCALE 1:20

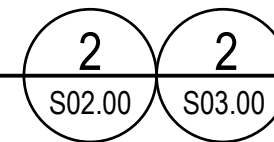

**This plan/document forms part of the
Approved Construction Certificate
F2022-100098
Issued By First Building Certifiers P/L BDC 3219**

Rev.	Date	Drawn	Eng	Description
A	19.05.23	C.L.	R.N.	ISSUED FOR CONSTRUCTION

CORDOR Pty. Limited
T/A ALDRED WU & ASSOCIATES

PO BOX 133
KILLARA, NSW 2071
M: 0411139 899
aldredwu@gmail.com

- THIS DRAWING IS THE COPYRIGHT OF NASTASI & ASSOCIATES CONSULTING CIVIL & STRUCTURAL ENGINEERS, Unit 5, 1-3 Whyalla Place, Prestons, 2170. PO Box 6048, Hammondville, NSW, 2170.
- IT IS NOT ALLOWED TO COPY OR REPRODUCE IT'S CONTENTS IN ANY FORM EXCEPT FOR THE PURPOSE WHICH IT IS INTENDED WITHOUT THE ABOVE CONSULTANT'S AUTHORITY.
- DO NOT SCALE THIS DRAWING, ONLY STATED DIMENSIONS ARE TO BE CONSIDERED.
- CONTRACTOR TO VERIFY THE DETAIL / INFORMATION GIVEN IN THIS DRAWING, ANY DISCREPANCIES SHALL BE BROUGHT TO ENGINEERS ATTENTION PRIOR TO COMMENCEMENT OF WORK, FAILURE TO COMPLY WITH THE ABOVE WILL BE CONTRACTORS LIABILITY.

NASTASI & ASSOCIATES
CONSULTING ENGINEERS

RESIDENTIAL - COMMERCIAL - INDUSTRIAL - INFRASTRUCTURE
STRUCTURAL - CIVIL - STORMWATER - GEOTECHNICAL - SURVEYING - SITE SERVICES
OPERATING IN - NSW - QLD - VIC - TAS

Head Office: Unit 5, 1-3 Whyalla Place, Prestons, NSW 2170
www.nastasiassociates.com.au
ABN: 45 533 226 008
Ph (02) 96072864

QUALITY CONTROL

DRAWN	DATE
C.L.	19.05.2023
DESIGNED	DATE
R.N.	19.05.2023
CHECKED	DATE

APPROVED:

S. Nastasi
S. NASTASI
B.E., M.I.E. AUST., CPENG

CLIENT:

PROJECT:

83 BRIXTON ROAD,
BERALA NSW 2141

TITLE:

**FOOTING & SLAB
DETAILS - SHEET 1**

DRAWING STATUS

ISSUED FOR CONSTRUCTION

SCALE (AT ORIGINAL SIZE)

AS NOTED

PROJECT NO.	DRAWING NO.	REVISION NO.
31734	S03.10	A

[illegible]

SCALE 1:20


3

S02.00


3

S03.00

[illegible]

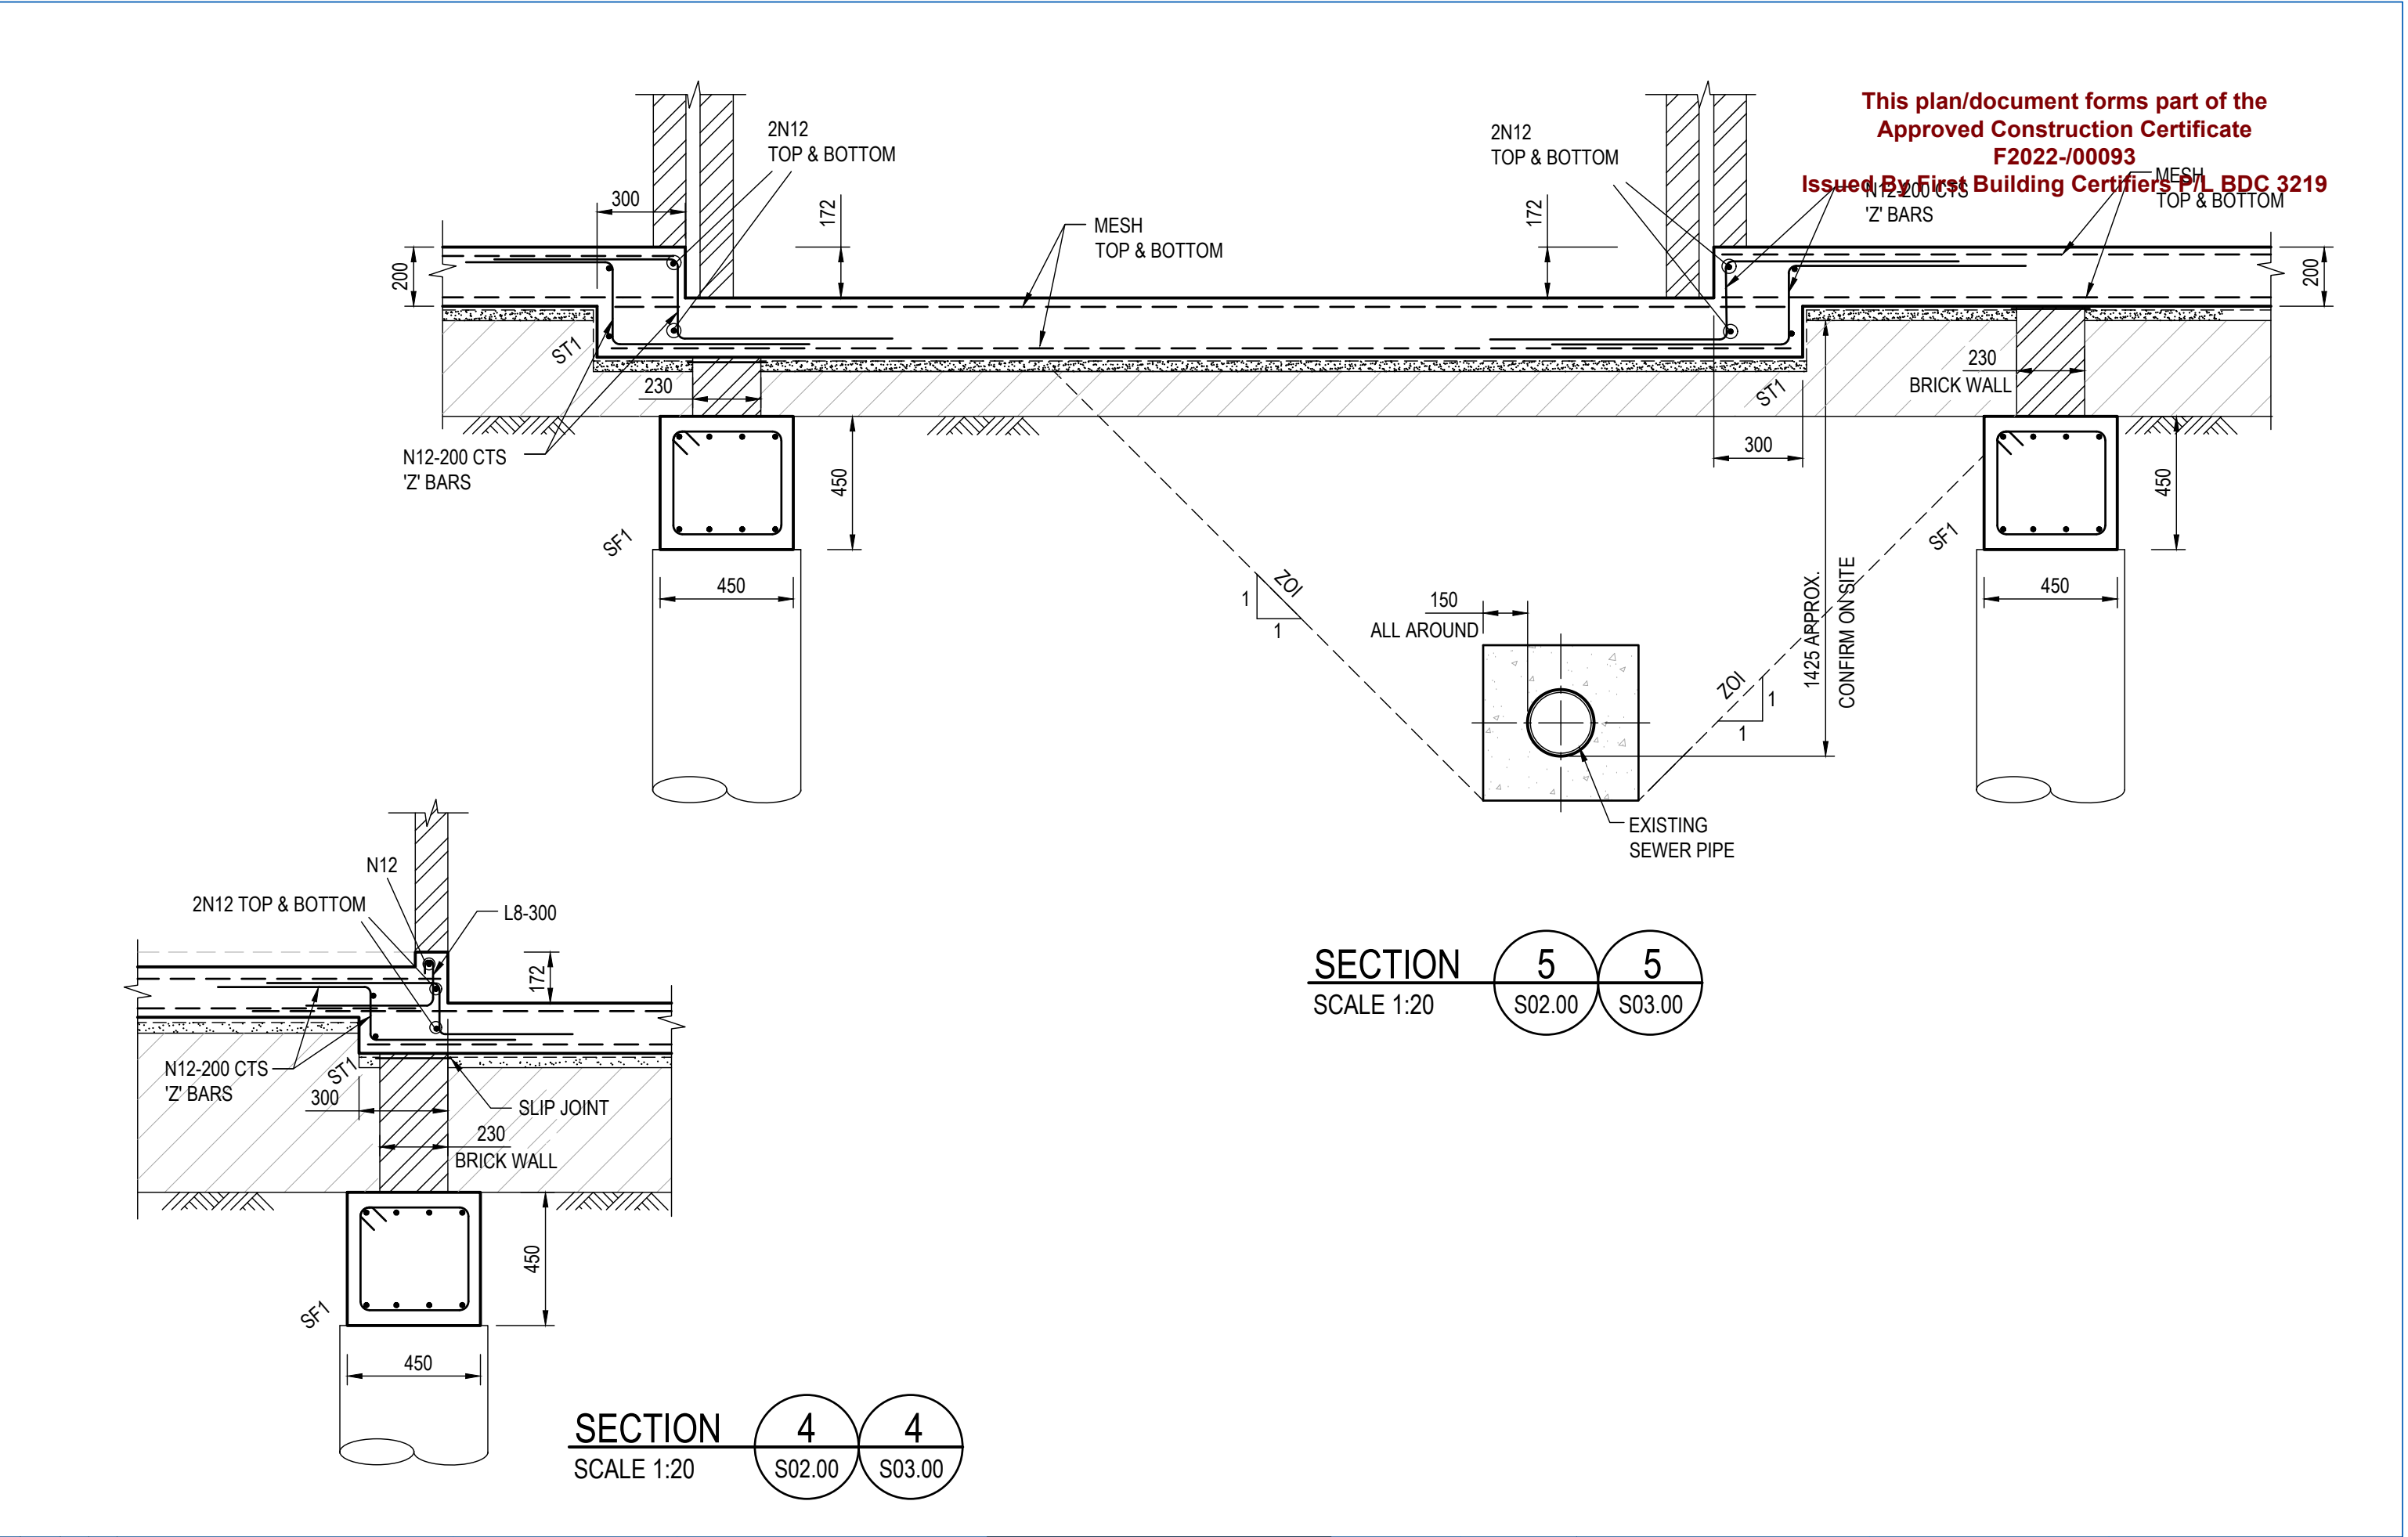


					CORDOR Pty. Limited T/A ALDRED WU & ASSOCIATES PO BOX 133 KILLARA, NSW 2071 M: 0411139 899 aldredwu@gmail.com	1. THIS DRAWING IS THE COPYRIGHT OF NASTASI & ASSOCIATES CONSULTING CIVIL & STRUCTURAL ENGINEERS, Unit 5, 1-3 Whyalla Place, Prestons, 2170. PO Box 6048, Hammondville, NSW, 2170. 2. IT IS NOT ALLOWED TO COPY OR REPRODUCE IT'S CONTENTS IN ANY FORM EXCEPT FOR THE PURPOSE WHICH IT IS INTENDED WITHOUT THE ABOVE CONSULTANT'S AUTHORITY. 3. DO NOT SCALE THIS DRAWING, ONLY STATED DIMENSIONS ARE TO BE CONSIDERED. 4. CONTRACTOR TO VERIFY THE DETAIL / INFORMATION GIVEN IN THIS DRAWING, ANY DISCREPANCIES SHALL BE BROUGHT TO ENGINEERS ATTENTION PRIOR TO COMMENCEMENT OF WORK, FAILURE TO COMPLY WITH THE ABOVE WILL BE CONTRACTORS LIABILITY.	NASTASI & ASSOCIATES CONSULTING ENGINEERS RESIDENTIAL - COMMERCIAL - INDUSTRIAL - INFRASTRUCTURE STRUCTURAL - CIVIL - STORMWATER - GEOTECHNICAL - SURVEYING - SITE SERVICES OPERATING IN - NSW - QLD - VIC - TAS Head Office: Unit 5, 1-3 Whyalla Place, Prestons, NSW 2170 www.nastasiassociates.com.au ABN - 45 533 226 008 Ph (02) 96072864	QUALITY CONTROL DRAWN DATE C.L. 19.05.2023 DESIGNED DATE R.N. 19.05.2023 CHECKED DATE	APPROVED: S. NASTASI B.E., M.I.E. AUST., CPENG	CLIENT: PROJECT: 83 BRIXTON ROAD, BERALA NSW 2141	TITLE: FOOTING & SLAB DETAILS - SHEET 3	DRAWING STATUS ISSUED FOR CONSTRUCTION SCALE (AT ORIGINAL SIZE) PROJECT NO. 31734 DRAWING NO. S03.12 REVISION NO. A
--	--	--	--	--	--	---	--	--	--	--	---	--

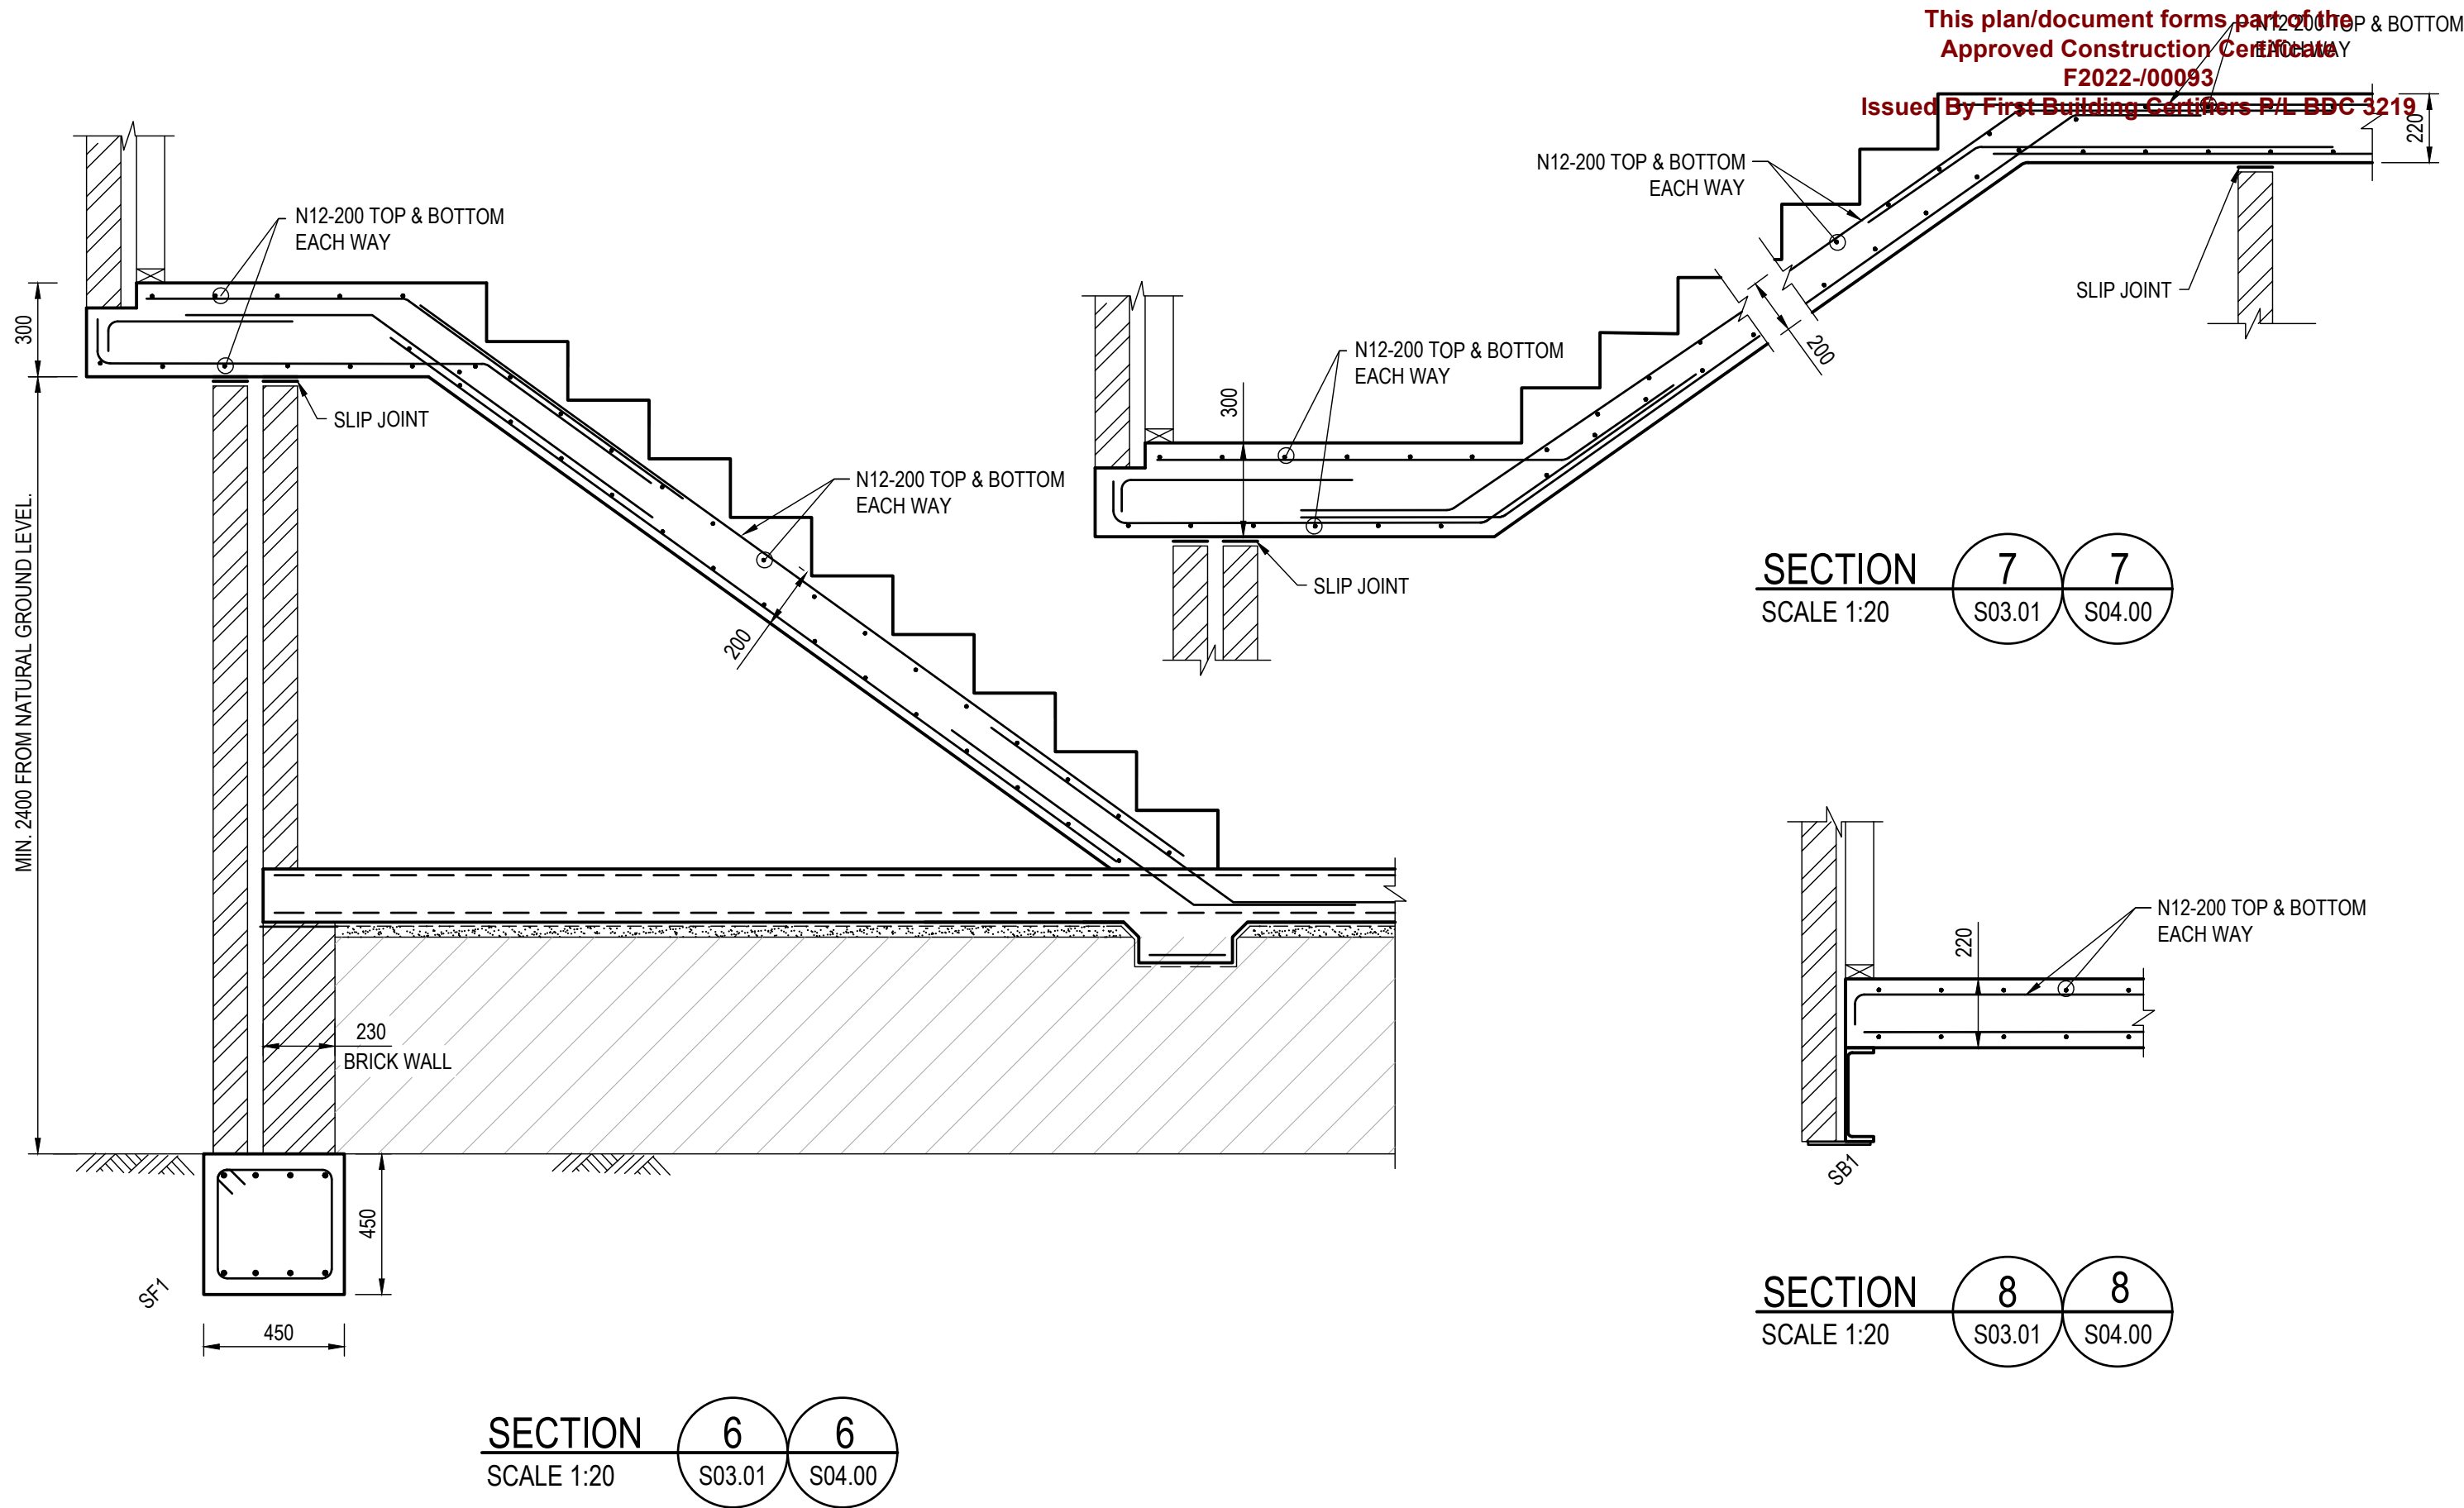

				CORDOR Pty. Limited TIA ALDRED WU & ASSOCIATES PO BOX 133 KILLARA, NSW 2071 M: 0411139 899 aldredwu@gmail.com		1. THIS DRAWING IS THE COPYRIGHT OF NASTASI & ASSOCIATES CONSULTING CIVIL & STRUCTURAL ENGINEERS, Unit 5, 1-3 Whyalla Place, Prestons, 2170. PO Box 6048, Hammondville, NSW, 2170. 2. IT IS NOT ALLOWED TO COPY OR REPRODUCE IT'S CONTENTS IN ANY FORM EXCEPT FOR THE PURPOSE WHICH IT IS INTENDED WITHOUT THE ABOVE CONSULTANT'S AUTHORITY. 3. DO NOT SCALE THIS DRAWING, ONLY STATED DIMENSIONS ARE TO BE CONSIDERED. 4. CONTRACTOR TO VERIFY THE DETAIL / INFORMATION GIVEN IN THIS DRAWING, ANY DISCREPANCIES SHALL BE BROUGHT TO ENGINEERS ATTENTION PRIOR TO COMMENCEMENT OF WORK, FAILURE TO COMPLY WITH THE ABOVE WILL BE CONTRACTORS LIABILITY.		NASTASI & ASSOCIATES CONSULTING ENGINEERS RESIDENTIAL - COMMERCIAL - INDUSTRIAL - INFRASTRUCTURE STRUCTURAL - CIVIL - STORMWATER - GEOTECHNICAL - SURVEYING - SITE SERVICES OPERATING IN - NSW - QLD - VIC - TAS Head Office: Unit 5, 1-3 Whyalla Place, Prestons, NSW 2170 www.nastasiassociates.com.au ABN : 45 533 226 008 Ph (02) 96072864		QUALITY CONTROL DRAWNDATE C.L.19.05.2023 DESIGNEDDATE R.N.19.05.2023 CHECKEDDATE		APPROVED:  S. NASTASI B.E., M.I.E. AUST., CPENG		CLIENT: PROJECT: 83 BRIXTON ROAD, BERALA NSW 2141		TITLE: STAIRS & LANDING SLAB DETAILS		DRAWING STATUS ISSUED FOR CONSTRUCTION SCALE (AT ORIGINAL SIZE) AS NOTED PROJECT NO. 31734 DRAWING NO. S03.13 REVISION NO. A	
A19.05.23 C.L. R.N. ISSUED FOR CONSTRUCTION Rev. Date Drawn Eng Description	

This plan/document forms part of the
Approved Construction Certificate
F2022-/00093
Issued By First Building Certifiers P/L BDC 3219

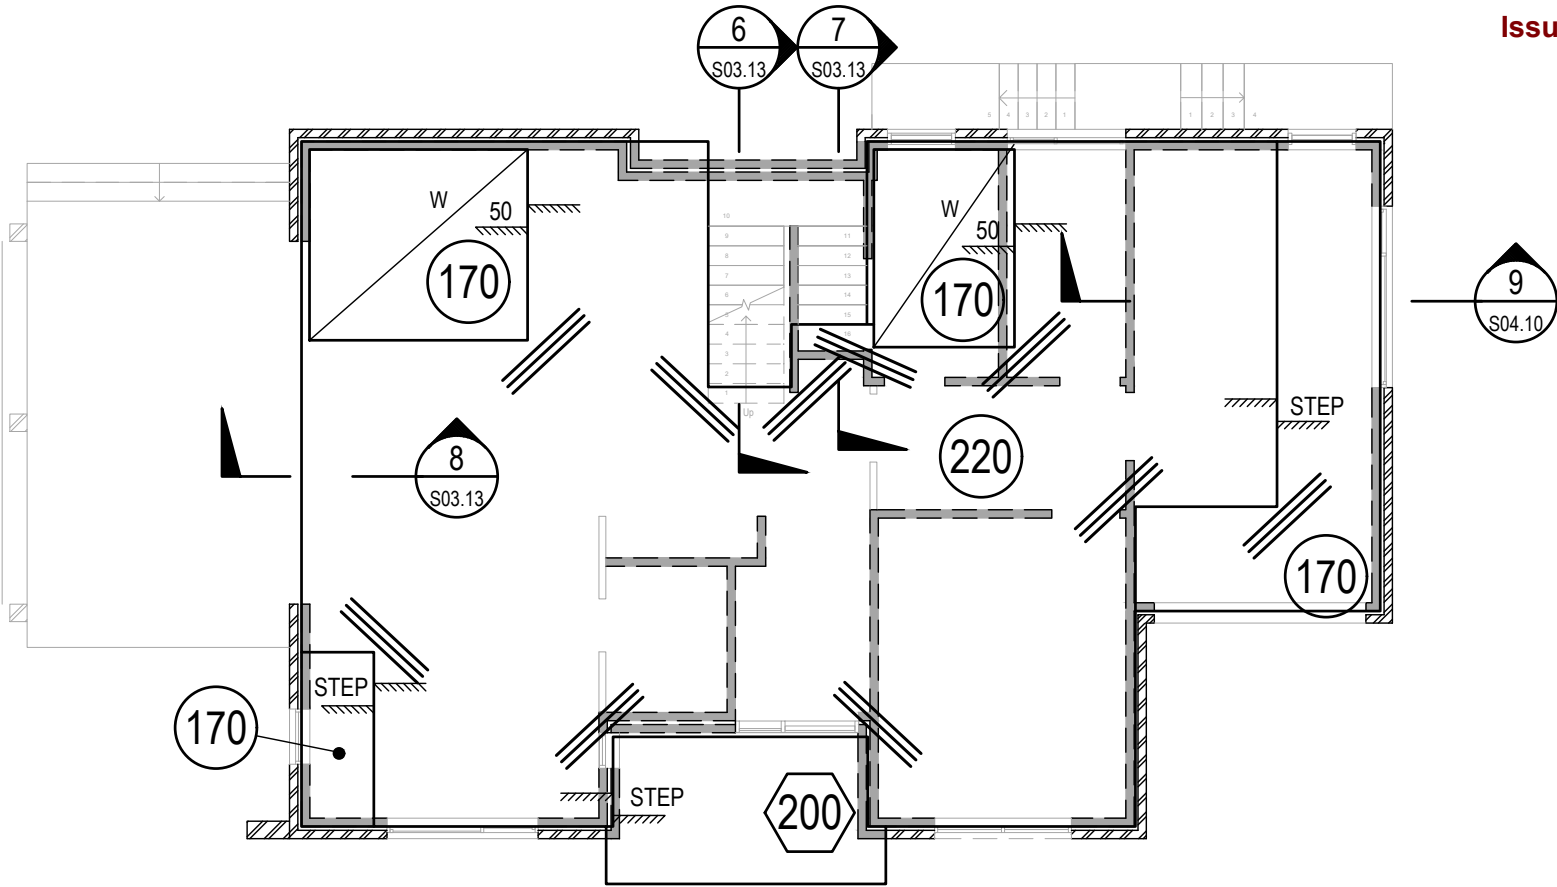

FIRST FLOOR SLAB PLAN


SCALE 1:100

NOTES:


- 170** - DENOTES CONCRETE SLAB THICKNESS.
REINFORCED WITH N12-200 CTS TOP & BOTTOM, EACH WAY.
- 220** - DENOTES CONCRETE SLAB THICKNESS
REINFORCED WITH N12-200 CTS TOP & BOTTOM, EACH WAY.
- 200** -DENOTES CONCRETE SLAB THICKNESS
REINFORCED WITH N12-200 CTS TOP & BOTTOM, EACH WAY

- STEP** - DENOTES SLAB STEP
- W** - DENOTES 50mm WET AREA SETDOWN.
- LOAD BEARING WALL UNDER**
- 3-N12 TRIMMING BARS(TOP) 2000 LONG**


REINFORCEMENT SEQUENCE

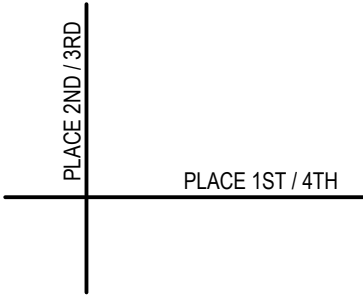


					CORDOR Pty. Limited T/A ALDRED WU & ASSOCIATES PO BOX 133 KILLARA, NSW 2071 M: 0411139 899 aldredwu@gmail.com	1. THIS DRAWING IS THE COPYRIGHT OF NASTASI & ASSOCIATES CONSULTING CIVIL & STRUCTURAL ENGINEERS, Unit 5, 1-3 Whyalla Place, Prestons, 2170. PO Box 6048, Hammondville, NSW, 2170. 2. IT IS NOT ALLOWED TO COPY OR REPRODUCE IT'S CONTENTS IN ANY FORM EXCEPT FOR THE PURPOSE WHICH IT IS INTENDED WITHOUT THE ABOVE CONSULTANT'S AUTHORITY. 3. DO NOT SCALE THIS DRAWING, ONLY STATED DIMENSIONS ARE TO BE CONSIDERED. 4. CONTRACTOR TO VERIFY THE DETAIL / INFORMATION GIVEN IN THIS DRAWING, ANY DISCREPANCIES SHALL BE BROUGHT TO ENGINEERS ATTENTION PRIOR TO COMMENCEMENT OF WORK, FAILURE TO COMPLY WITH THE ABOVE WILL BE CONTRACTORS LIABILITY.	NASTASI & ASSOCIATES CONSULTING ENGINEERS RESIDENTIAL - COMMERCIAL - INDUSTRIAL - INFRASTRUCTURE STRUCTURAL - CIVIL - STORMWATER - GEOTECHNICAL - SURVEYING - SITE SERVICES OPERATING IN - NSW - QLD - VIC - TAS Head Office: Unit 5, 1-3 Whyalla Place, Prestons, NSW 2170 www.nastasiassociates.com.au ABN: 45 533 226 008 Ph (02) 96072864	QUALITY CONTROL DRAWN DATE C.L. 19.05.2023 DESIGNED DATE R.N. 19.05.2023 CHECKED DATE	APPROVED: S. NASTASI B.E., M.I.E. AUST., CPENG	CLIENT: PROJECT: 83 BRIXTON ROAD, BERALA NSW 2141	TITLE: FIRST FLOOR SLAB PLAN	DRAWING STATUS ISSUED FOR CONSTRUCTION SCALE (AT ORIGINAL SIZE) AS NOTED PROJECT NO. 31734 DRAWING NO. S04.00 REVISION NO. A
--	--	--	--	--	---	---	--	---	---	--	---	---

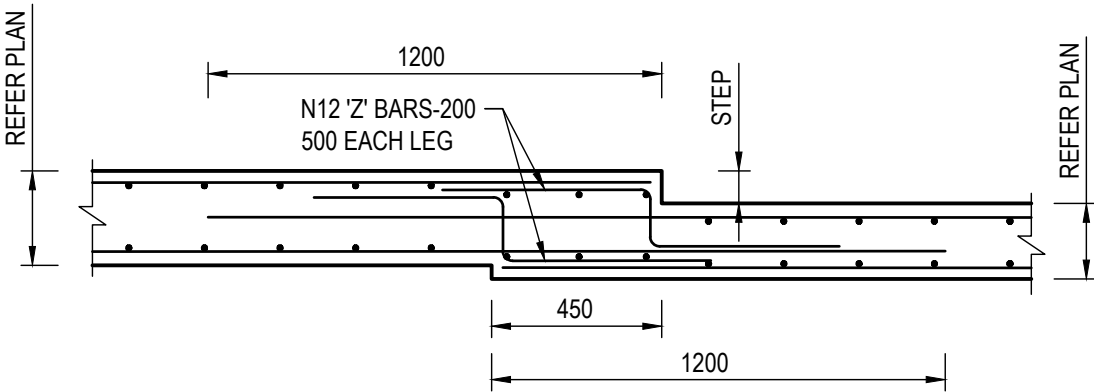

TYPICAL FOLD/STEP DETAIL
SCALE 1:20

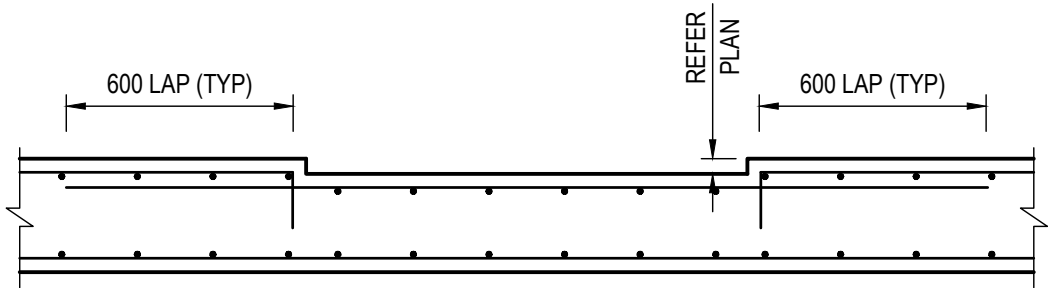

TYPICAL WET AREA SETDOWN DETAIL
SCALE 1:20

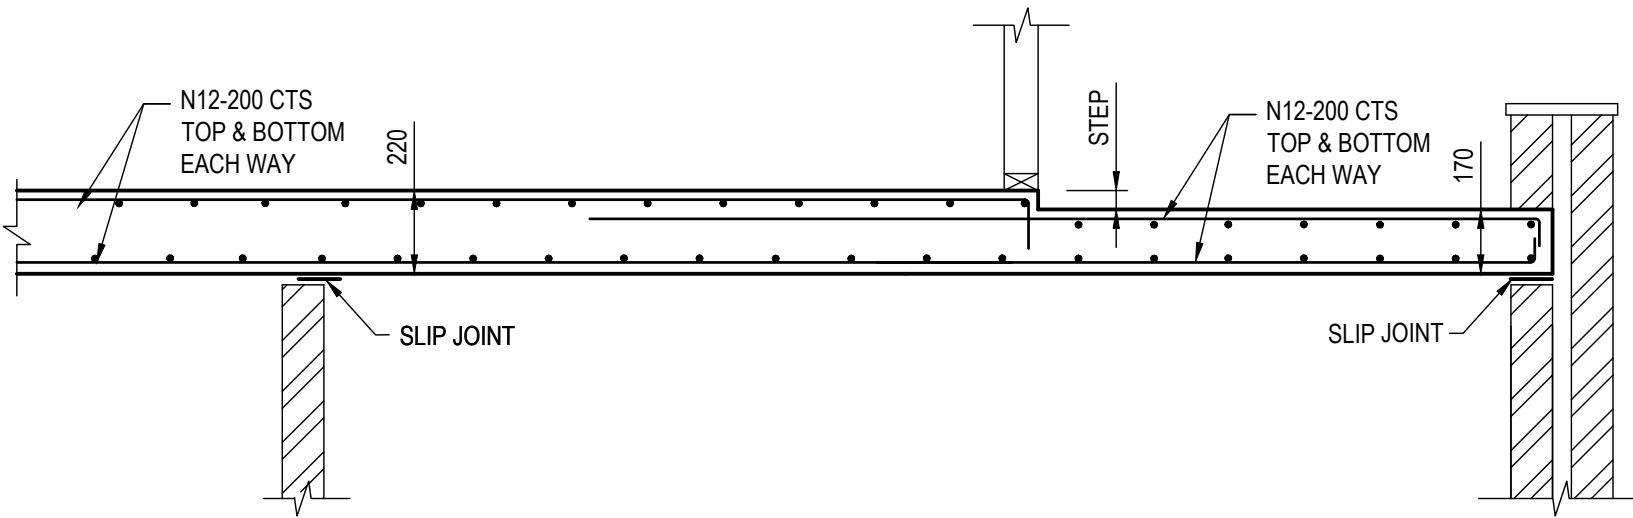


SECTION 9
SCALE 1:20

9
S04.00

				CORDOR Pty. Limited T/A ALDRED WU & ASSOCIATES PO BOX 133 KILLARA, NSW 2071 M: 0411139 899 aldredwu@gmail.com	1. THIS DRAWING IS THE COPYRIGHT OF NASTASI & ASSOCIATES CONSULTING CIVIL & STRUCTURAL ENGINEERS, Unit 5,1-3 Whyalla Place,Prestons, 2170. PO Box 6048, Hammondville, NSW, 2170. 2. IT IS NOT ALLOWED TO COPY OR REPRODUCE IT'S CONTENTS IN ANY FORM EXCEPT FOR THE PURPOSE, WHICH IT IS INTENDED WITHOUT THE ABOVE CONSULTANT'S AUTHORITY. 3. DO NOT SCALE THIS DRAWING, ONLY STATED DIMENSIONS ARE TO BE CONSIDERED. 4. CONTRACTOR TO VERIFY THE DETAIL / INFORMATION GIVEN IN THIS DRAWING, ANY DISCREPANCIES SHALL BE BROUGHT TO ENGINEERS ATTENTION PRIOR TO COMMENCEMENT OF WORK, FAILURE TO COMPLY WITH THE ABOVE WILL BE CONTRACTORS LIABILITY.	 NASTASI & ASSOCIATES CONSULTING ENGINEERS RESIDENTIAL - COMMERCIAL - INDUSTRIAL - INFRASTRUCTURE STRUCTURAL - CIVIL - STORMWATER - GEOTECHNICAL - SURVEYING - SITE SERVICES OPERATING IN - NSW - QLD - VIC - TAS Head Office: Unit 5, 1-3 Whyalla Place, Prestons, NSW 2170 www.nastasiassociates.com.au ABN : 45 533 226 008 Ph (02) 96072864	QUALITY CONTROL DRAWN DATE C.L. 19.05.2023 DESIGNED DATE R.N. 19.05.2023 CHECKED DATE	APPROVED:  S. NASTASI B.E.,M.I.E. AUST, CPENG	CLIENT: PROJECT: 83 BRIXTON ROAD, BERALA NSW 2141	TITLE: FIRST FLOOR SLAB DETAILS	DRAWING STATUS ISSUED FOR CONSTRUCTION SCALE (AT ORIGINAL SIZE) AS NOTED PROJECT NO. 31734 DRAWING NO. S04.10 REVISION NO. A
A	19.05.23	C.L.	R.N.				ISSUED FOR CONSTRUCTION				
Rev.	Date	Drawn	Eng				Description				

**This plan/document forms part of the
Approved Construction Certificate
F2022-/00093
Issued By First Building Certifiers P/L BDC 3219**

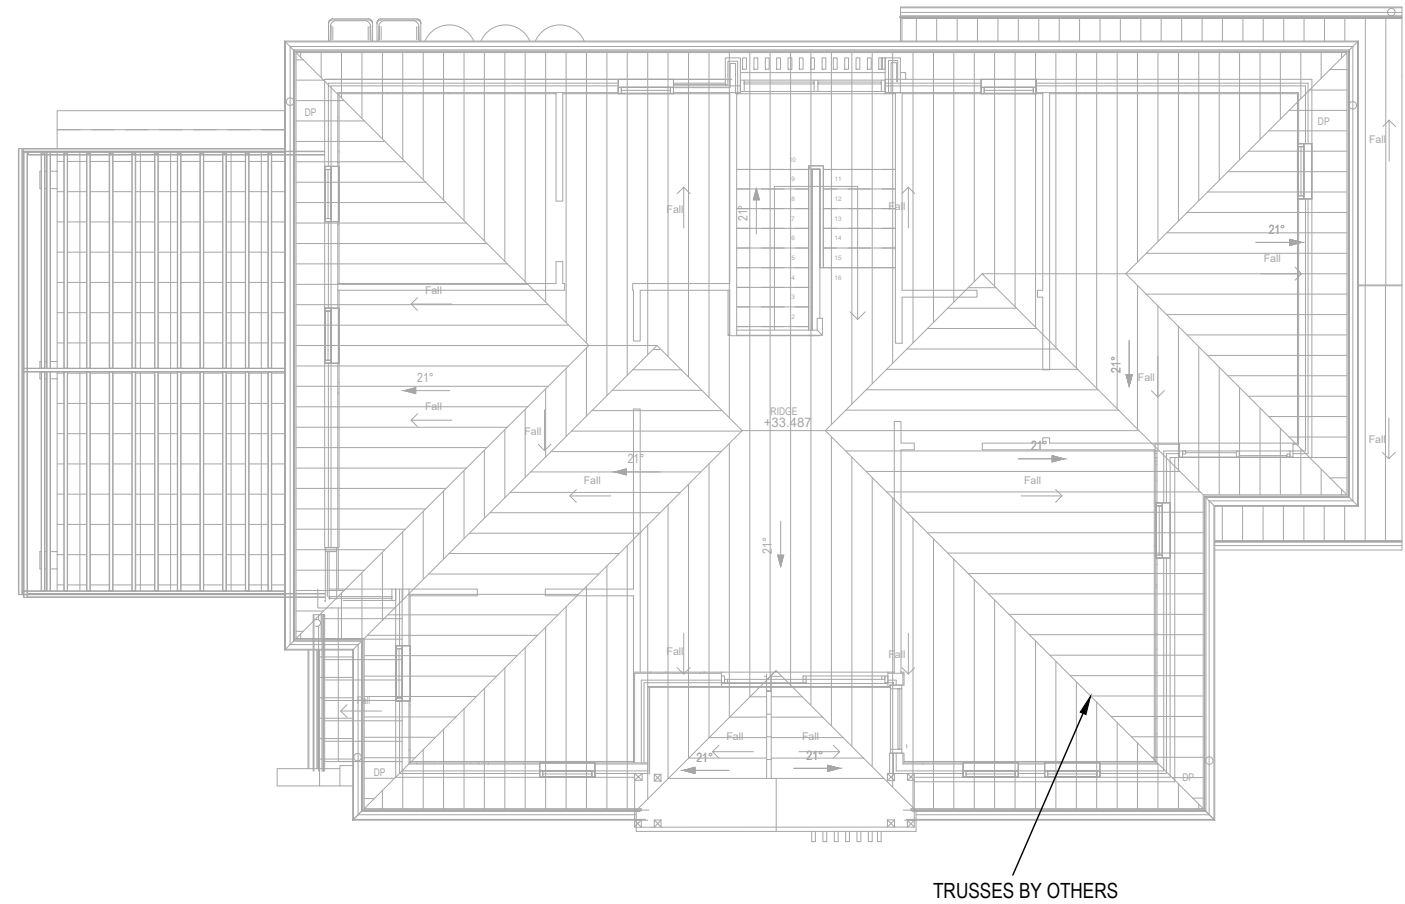

ROOF PLAN

SCALE 1:100

[illegible]