

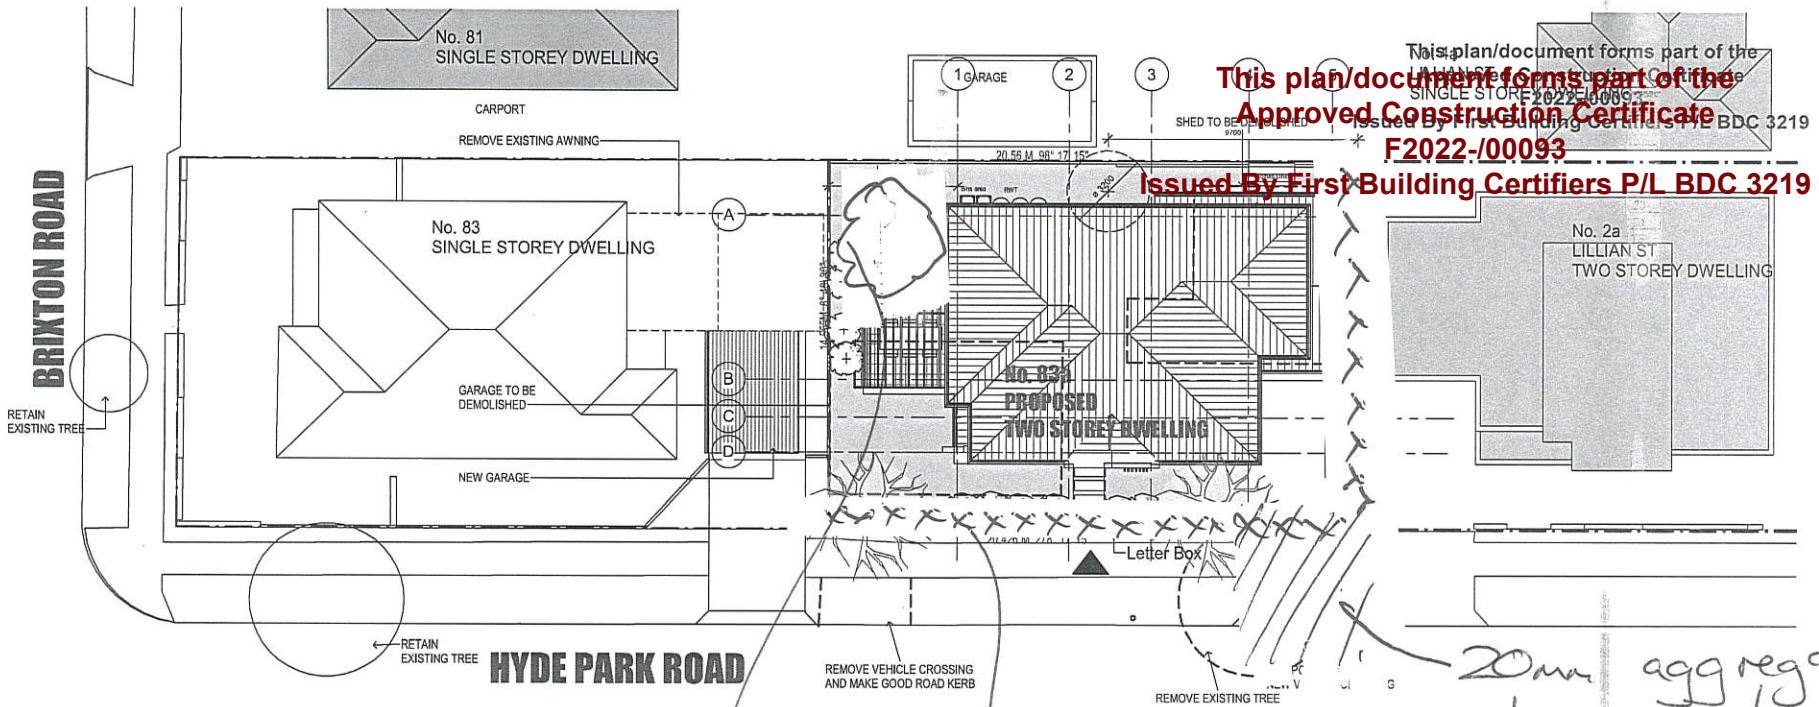


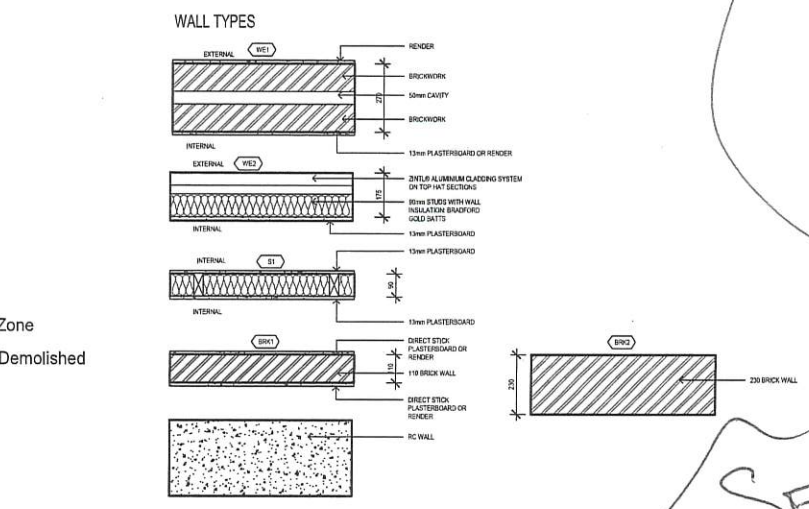

This plan/document forms part of the
 LILLIAN ST SINGLE STOREY DWELLING
 Issued By First Building Certifiers P/L BDC 3219
F2022-/00093

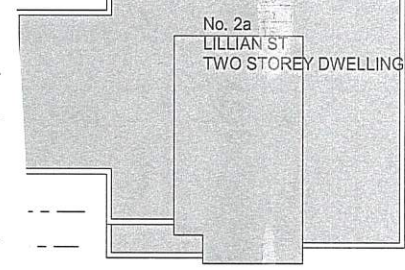

- LEGEND**
- ▶ Pedestrian
 - ▶ Entry Vehicle
 - Entry
 - Trees To Be Removed
 - Trees To Be Retained
 - New Planted Trees
 - Structural Root Zone
 - Building To Be Demolished

20mm aggregate entry point

Sediment Erosion Control Barrier

Stockpile of Soil

SEDIMENT EROSION CONTROL PLAN

GENERAL NOTES

- All dimensions shall be taken in preference to scaling.
- Verify all dimensions and levels on site prior to commencement of work or activity.
- All drawings to be made in accordance with information contained on the first page.
- Verify any and all measurements, the indicated before proceeding with the work.
- All materials and construction methods to comply with relevant codes, applicable standards and manufacturer's instructions.
- All construction to be completed and verified in accordance with the relevant codes.
- The Builder to retain and store all certificates of compliance with NCC for the duration of the project.

ISSUE FOR CCA

YOU DIG

SITE PLAN

83 BRIXTON ROAD, BERALA
EXISTING DWELLING
CUMBERLAND COUNCIL


GENERAL NOTES

- Figure dimensions shall be taken in preference to scaling.
- Drawing to be read in conjunction with information on the first page.
- Check all dimensions and levels on site prior to commencement of work.
- All workmanship and materials shall comply with all relevant codes, standards, Australian Standards and manufacturer's instructions.
- All existing ground lines and trees locations are approximate and are to be verified on-site by Builder.
- Unless noted Issued for construction drawing not to be used for construction.



This drawing and information contained in this drawing is a subject to COPYRIGHT and should not be reproduced in part or in whole without an expressed permission of

RJK ARCHITECTS Pty. Ltd.
 PO Box 304 Annandale NSW 2038
 P: (02) 8084 4435 E: admin@rjkarchitects.com.au
 Nominated Architect: Jiri Kure Reg. No. 7616

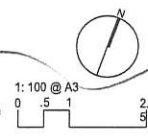

ISSUE	AMENDMENT	DATE	DRAWN	CHECKED
B	Issue for CC	25.04.23	DC	AW
A	Issue for Development Application	19.02.21	GS	JK

DWG NO.
CC02
 ISSUE
B