

LEGEND:

	SEWER MAIN AND DIRECTION OF FLOW		POTABLE WATER MAIN	VC	VITRIFIED CLAY
	SYDNEY WATER SEWER MAN-HOLE		HYDRANT	S.O.	SQUARE OFF
	MAINTENANCE SHAFT		STOP VALVE	PEG	PEG IN GOUND
	RODDING POINT		DICL DUCTILE IRON CEMENT LINED	NAIL	NAIL IN GROUND OR ON WALL
	VENTSHAFT (INDUCT OR EDUCT)		EW EARTHENWARE	BDY	BOUNDARY
	VERTICAL RISER		RC REINFORCED CONCRETE	EX.	EXISTING
	P.C.P. OR JUNCTION		SGW SALT GLAZED WARE	DN	DIAMETER
					PEG


PEG-OUT / SERVICE PROTECTION REPORT

A3 - SIZE SHEET

ELECTRONIC DETECTION USED TO LOCATE SEWER MAIN ON SITE.

NOTES:

- CONTRACTOR TO CONFIRM LINE, LEVEL AND SIZE OF ALL THE EXISTING SERVICES (AS PER NOTE ON PLAN) WITHIN THE VICINITY OF ANY NEW WORKS AND REPORT ANY CONFLICT TO SITE SUPERINTENDENT PRIOR TO ANY CONSTRUCTION COMMENCING
- Ausflow PTY LTD (ABN: 86 097 766 428)
Ph: (02) 9555 7979
Level 1, 323a Darling Street, Balmain NSW 2041
Email: info@ausflowsydney.com.au
Web: www.ausflowsydney.com.au
ACCREDITED AS SERVICE PROTECTION REPORTER BY SYDNEY WATER
- THE LOCATION OF THE ASSETS SPECIFIED ON THIS REPORT HAVE BEEN TAKEN FROM EXISTING FENCE LINES AND/OR SURVEYORS MARKINGS OR PEGS. FENCE LINES MAY NOT BE TRUE BOUNDARY LINES AND MAY NEED TO BE CONFIRMED BY SURVEYOR.
- THIS PLAN IS NOT TO SCALE, DO NOT SCALE FROM THIS PLAN REFER DIMENSIONS SHOWN

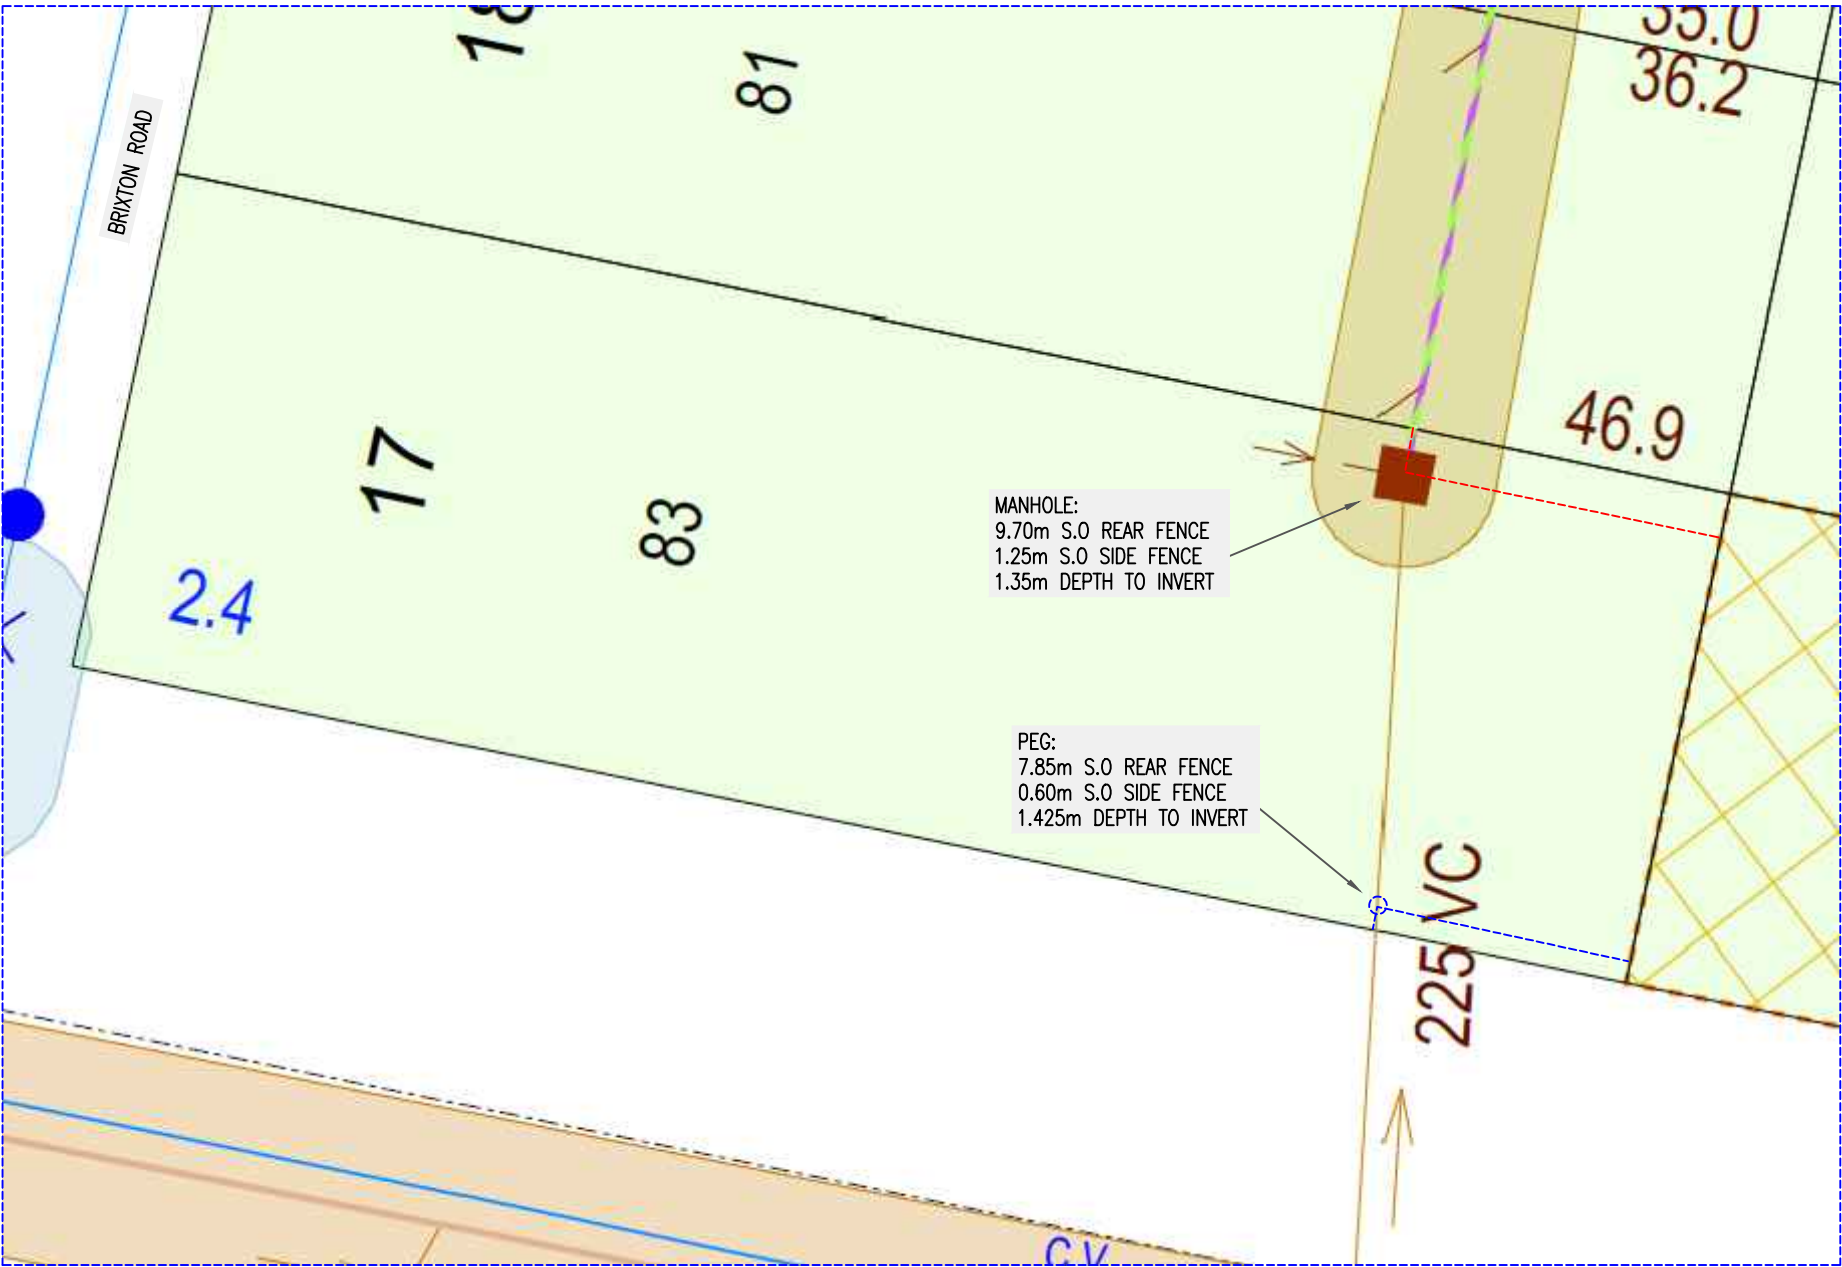

DRAFTED BY: PG/GJ/CO

PLAN TO BE READ IN CONJUNCTION WITH CURRENT SURVEY PLAN	UTILITIES LOCATED:				SITE STRATA (CIRCLE APPLICABLE)							PROPERTY ADDRESS:		PLAN SUPPLIED BY:		
	SERVICE	DATE	SIZE (mm)	TYPE	CLAY	ROCK	ROCK TRENCH	SAND	SHALE	TUNNEL	RUBBISH FILL	OTHER (SPECIFY)	LOT: 17 No. 83 Street name: Brixton Road, Suburb: Berala			
PRIOR TO COMMENCEMENT OF EXCAVATION FOR PROPOSED AND / OR EXISTING SERVICES CONTACT:	EXISTING SEWER:	17/10/22	225	VC									SHEET 1 OF 1			
DIAL BEFORE YOU DIG Ph. 1100 ELECTRICITY AUSGRID Ph. 4951 4555 GAS AGILITY Ph. 132 909 TELECOMM. TELSTRA Ph. 9204 0880 GIVE AT LEAST 48 HOURS NOTICE	COUNCIL STORM WATER ASSET:				I Gabriel Austin, of Ausflow Pty Ltd, being accredited to carry out a Service Protection Report, certify that the information shown on the report is accurate and has been prepared in accordance with the relevant instructions. LOCATOR: Gabriel Austin LOCATOR SIGNATURE: 											
	STORMWATER: SWD															
	POTABLE WATER:															