


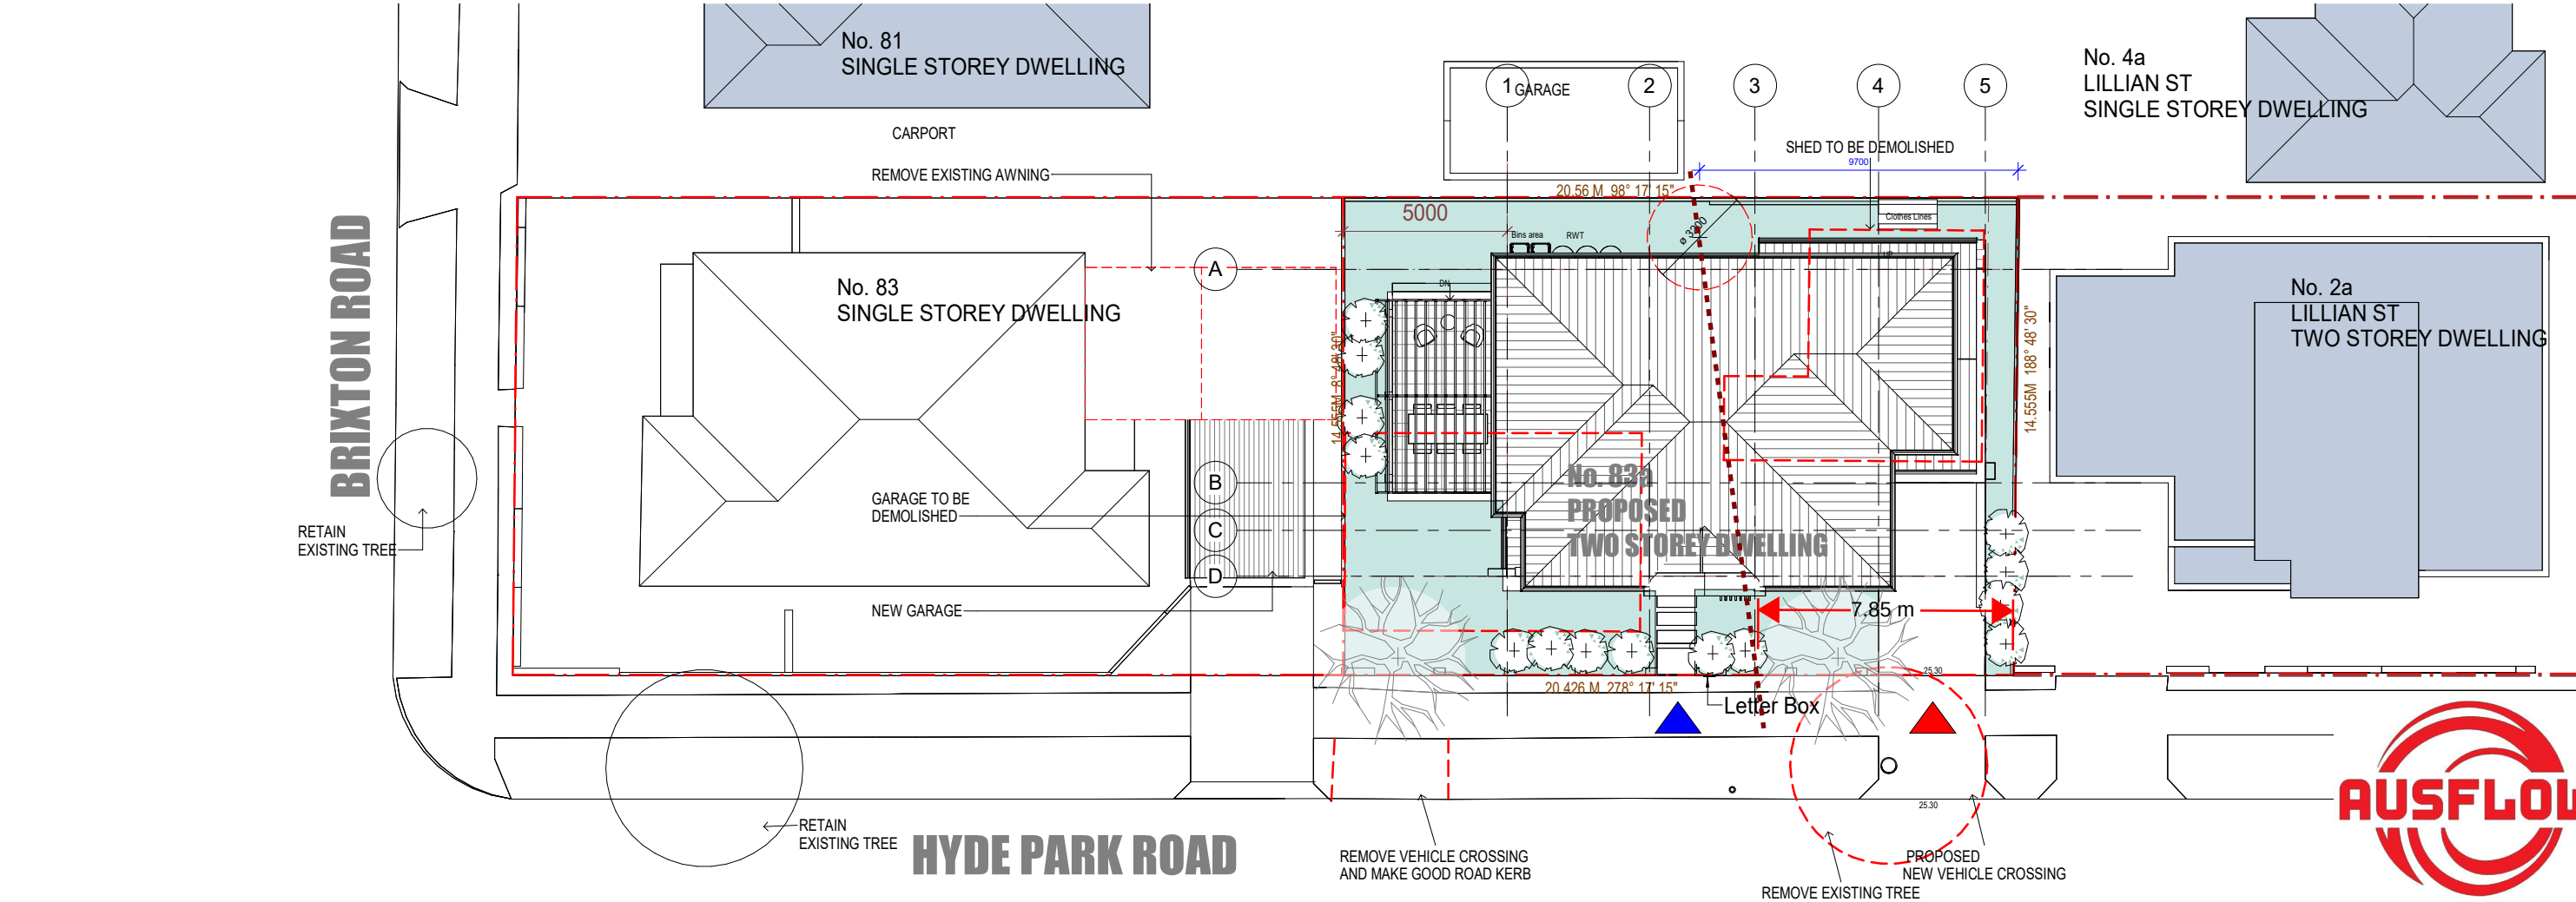

BUILDING PLAN APPROVED:
INSPECTIONS REQUIRED

- ☒ CONCRETE ENCASEMENT
- ☒ PIER FOUNDATION
- ☐ SIDE LINE / JUNCTION
- ☐ GENERAL SITE

BOOK YOUR INSPECTION 48hrs PRIOR TO WORKS
COMMENCING Call (02) 9555 7979

Accredited Supplier to SYDNEY WATER

**BUILDING PLAN APPROVED
SUBJECT TO REQUIREMENTS**

Ref No: **1650950** Date: **18/5/23**


- GENERAL NOTES:
- Figured dimensions shall be taken in preference to scaling
 - Verify all dimensions and levels on site prior to commencement of work or ordering materials.
 - All drawing to be read in conjunction with information contained on the first page.
 - Verify any and all discrepancies with the Architect before proceeding with the works.
 - All materials and construction methods to comply with relevant codes, applicable standards and manufacturer's instructions.
 - For construction purposes only use drawing clearly labeled "FOR CONSTRUCTION"
 - The builder to collect and retain all certificates of compliance with NCC for materials used during construction



ISSUE FOR CCA
FOR CONSTRUCTION CERTIFICATE APPLICATION ONLY
NOT FOR CONSTRUCTION

- LEGEND**
- Pedestrian
 - Entry Vehicle
 - Entry
 - Trees To Be Removed
 - Trees To Be Retained
 - New Planted
 - Trees Structural Root Zone
 - Building To Be Demolished

WALL TYPES

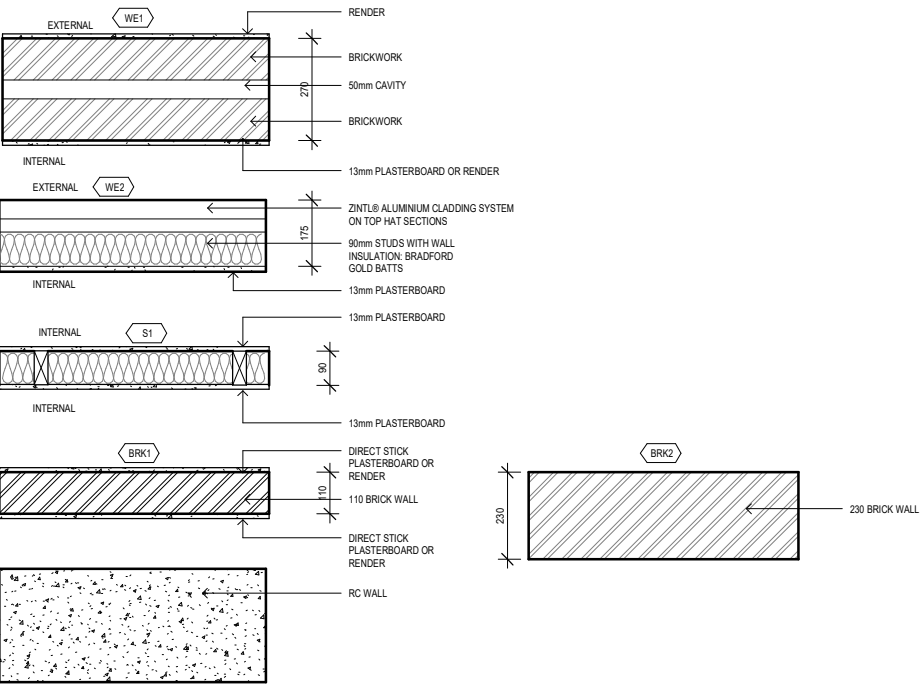

SITE PLAN


83 BRIXTON ROAD, BERALA
EXISTING DWELLING
CUMBERLAND COUNCIL

- GENERAL NOTES
- Figured dimensions shall be taken in preference to scaling
 - Drawing to be read in conjunction with information on the first page
 - Check all dimensions and levels on site prior to commencement of works
 - All workmanship and materials shall comply with all relevant codes, ordinances, Australian Standards and manufacturers instructions
 - All existing ground lines and trees locations are approximate and are to be verified on-site by Builder
 - Unless noted Issued for construction* drawing not to be used for construction



This drawing and information contained in this drawing is a subject to COPYRIGHT and should not be reproduced in part or in whole without an expressed permission of:

RJK ARCHITECTS Pty. Ltd.
PO Box 304 Annandale NSW 2038
P: (02) 8084 4435 E: admin@rjkarchitects.com.au
Nominated Architect : Jiri Kure Reg. No. 7616


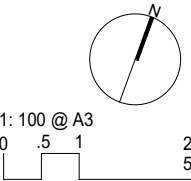


ISSUE	AMENDMENT	DATE	DRAWN	CHECKED
B	Issue for CC	25.04.23	DC	AW
A	Issue for Development Application	19.02.21	GS	JK

DWG NO.
CC02

ISSUE
B

ACCESS PATH TO MANHOLE
FROM STREET FRONTAGE

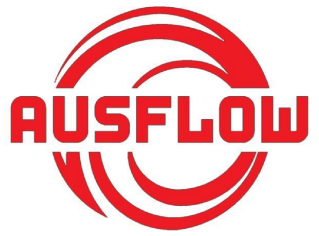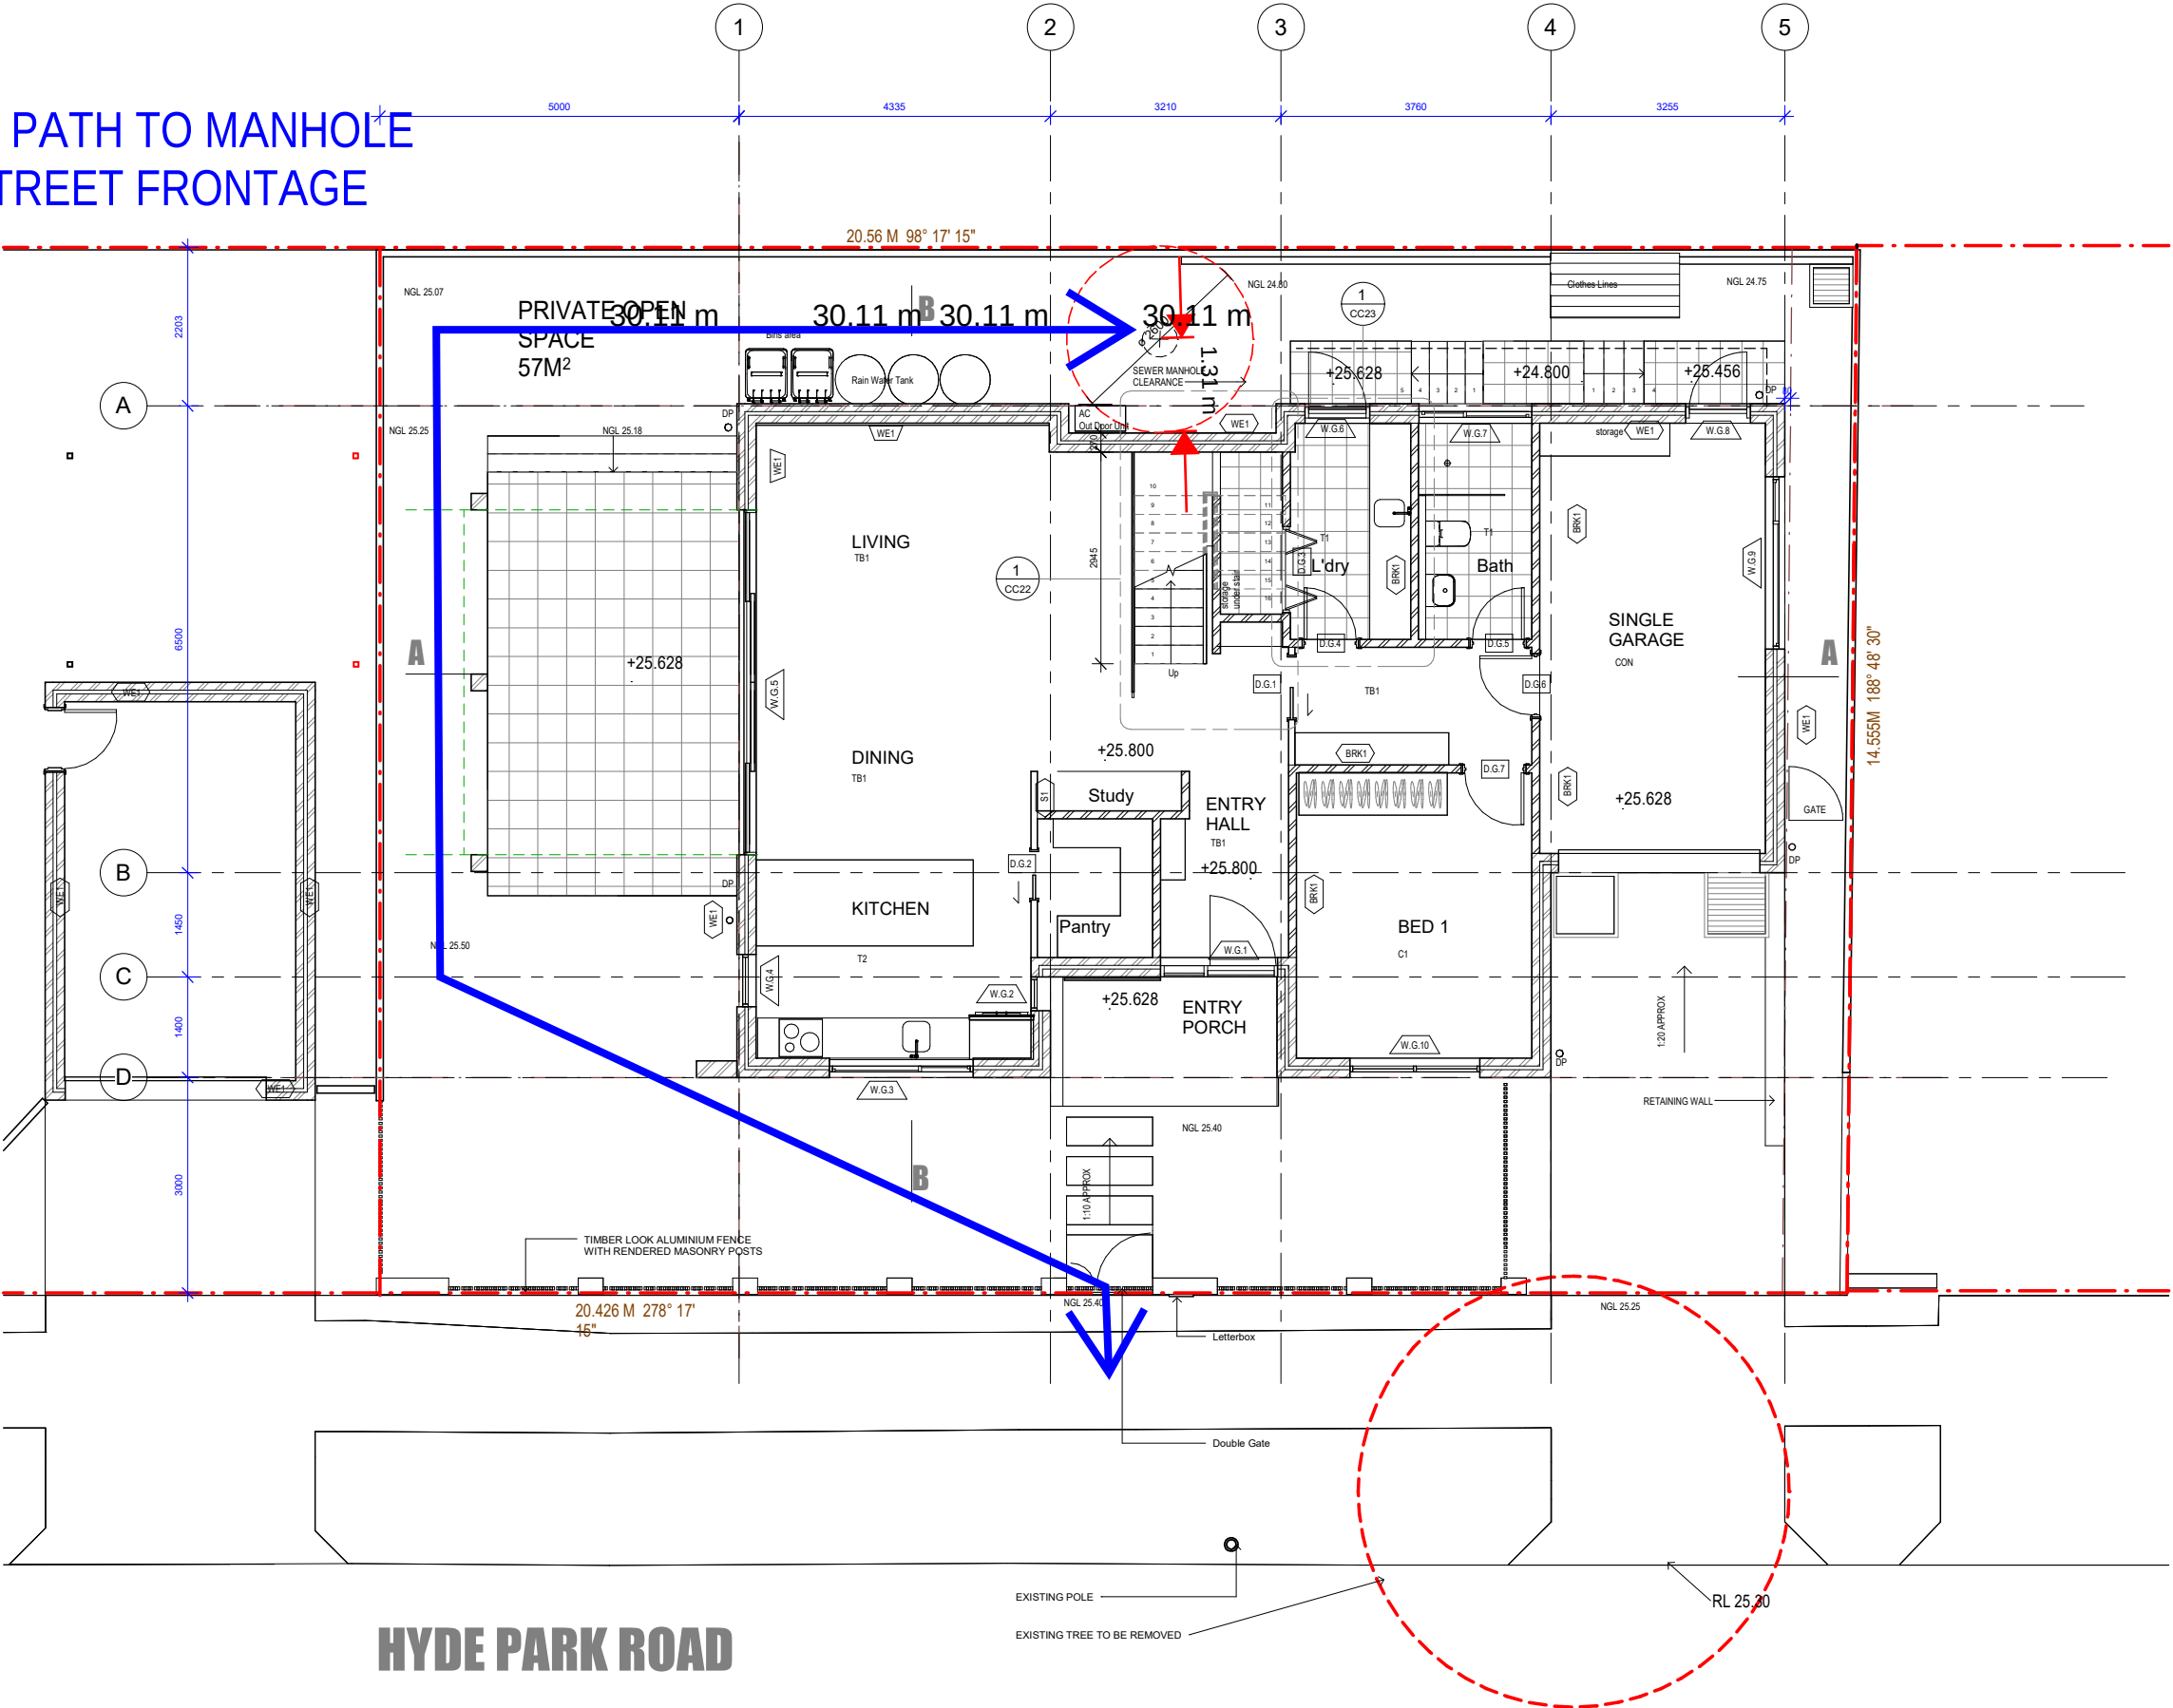

BUILDING PLAN APPROVED:
INSPECTIONS REQUIRED

- ☒ CONCRETE ENCASEMENT
- ☒ PIER FOUNDATION
- ☐ SIDE LINE / JUNCTION
- ☐ GENERAL SITE

BOOK YOUR INSPECTION 48hrs PRIOR TO WORKS
COMMENCING Call (02) 9555 7979

Accredited Supplier to SYDNEY WATER

BUILDING PLAN APPROVED
SUBJECT TO REQUIREMENTS

Ref No: 1650950 Date: 18/5/23

FLOOR FINISHES LEGEND:

- T1 CERAMIC TILES
- T2 CERAMIC TILES
- TB1 TIMBER FLOOR
- CON CONCRETE FINISH
- C1 CARPET

- GENERAL NOTES:
- Figured dimensions shall be taken in preference to scaling.
 - Verify all dimensions and levels on site prior to commencement of work or ordering materials.
 - All drawing to be read in conjunction with information contained on the first page.
 - Verify any and all discrepancies with the Architect before proceeding with the works.
 - All materials and construction methods to comply with relevant codes, applicable standards and manufacturer's instructions.
 - For construction purposes only use drawing clearly labeled "FOR CONSTRUCTION".
 - The builder to collect and retain all certificates of compliance with NCC for materials used during construction.



ISSUE FOR CCA
FOR CONSTRUCTION CERTIFICATE APPLICATION ONLY
NOT FOR CONSTRUCTION

GROUND FLOOR

83 BRIXTON ROAD, BERALA
EXISTING DWELLING


CUMBERLAND COUNCIL

- GENERAL NOTES
- Figured dimensions shall be taken in preference to scaling
 - Drawing to be read in conjunction with information on the first page
 - Check all dimensions and levels on site prior to commencement of works
 - All workmanship and materials shall comply with all relevant codes, ordinances, Australian Standards and manufacturers instructions
 - All existing ground lines and trees locations are approximate and are to be verified on-site by Builder
 - Unless noted Issued for construction* drawing not to be used for construction



This drawing and information contained in this drawing is a subject to COPYRIGHT and should not be reproduced in part or in whole without an expressed permission of:

RJK ARCHITECTS Pty. Ltd.
PO Box 304 Annandale NSW 2038
P: (02) 8084 4435 E: admin@rjkarchitects.com.au
Nominated Architect : Jiri Kure Reg. No. 7616

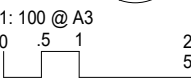

ISSUE	AMENDMENT	DATE	DRAWN	CHECKED
B	Issue for CC	25.04.23	DC	AW
A	Issue for Development Application	19.02.21	GS	JK

DWG NO.
CC04

ISSUE
B